


Projeto • PRÉDIO 01



Localização: Vitória da Conquista - BA

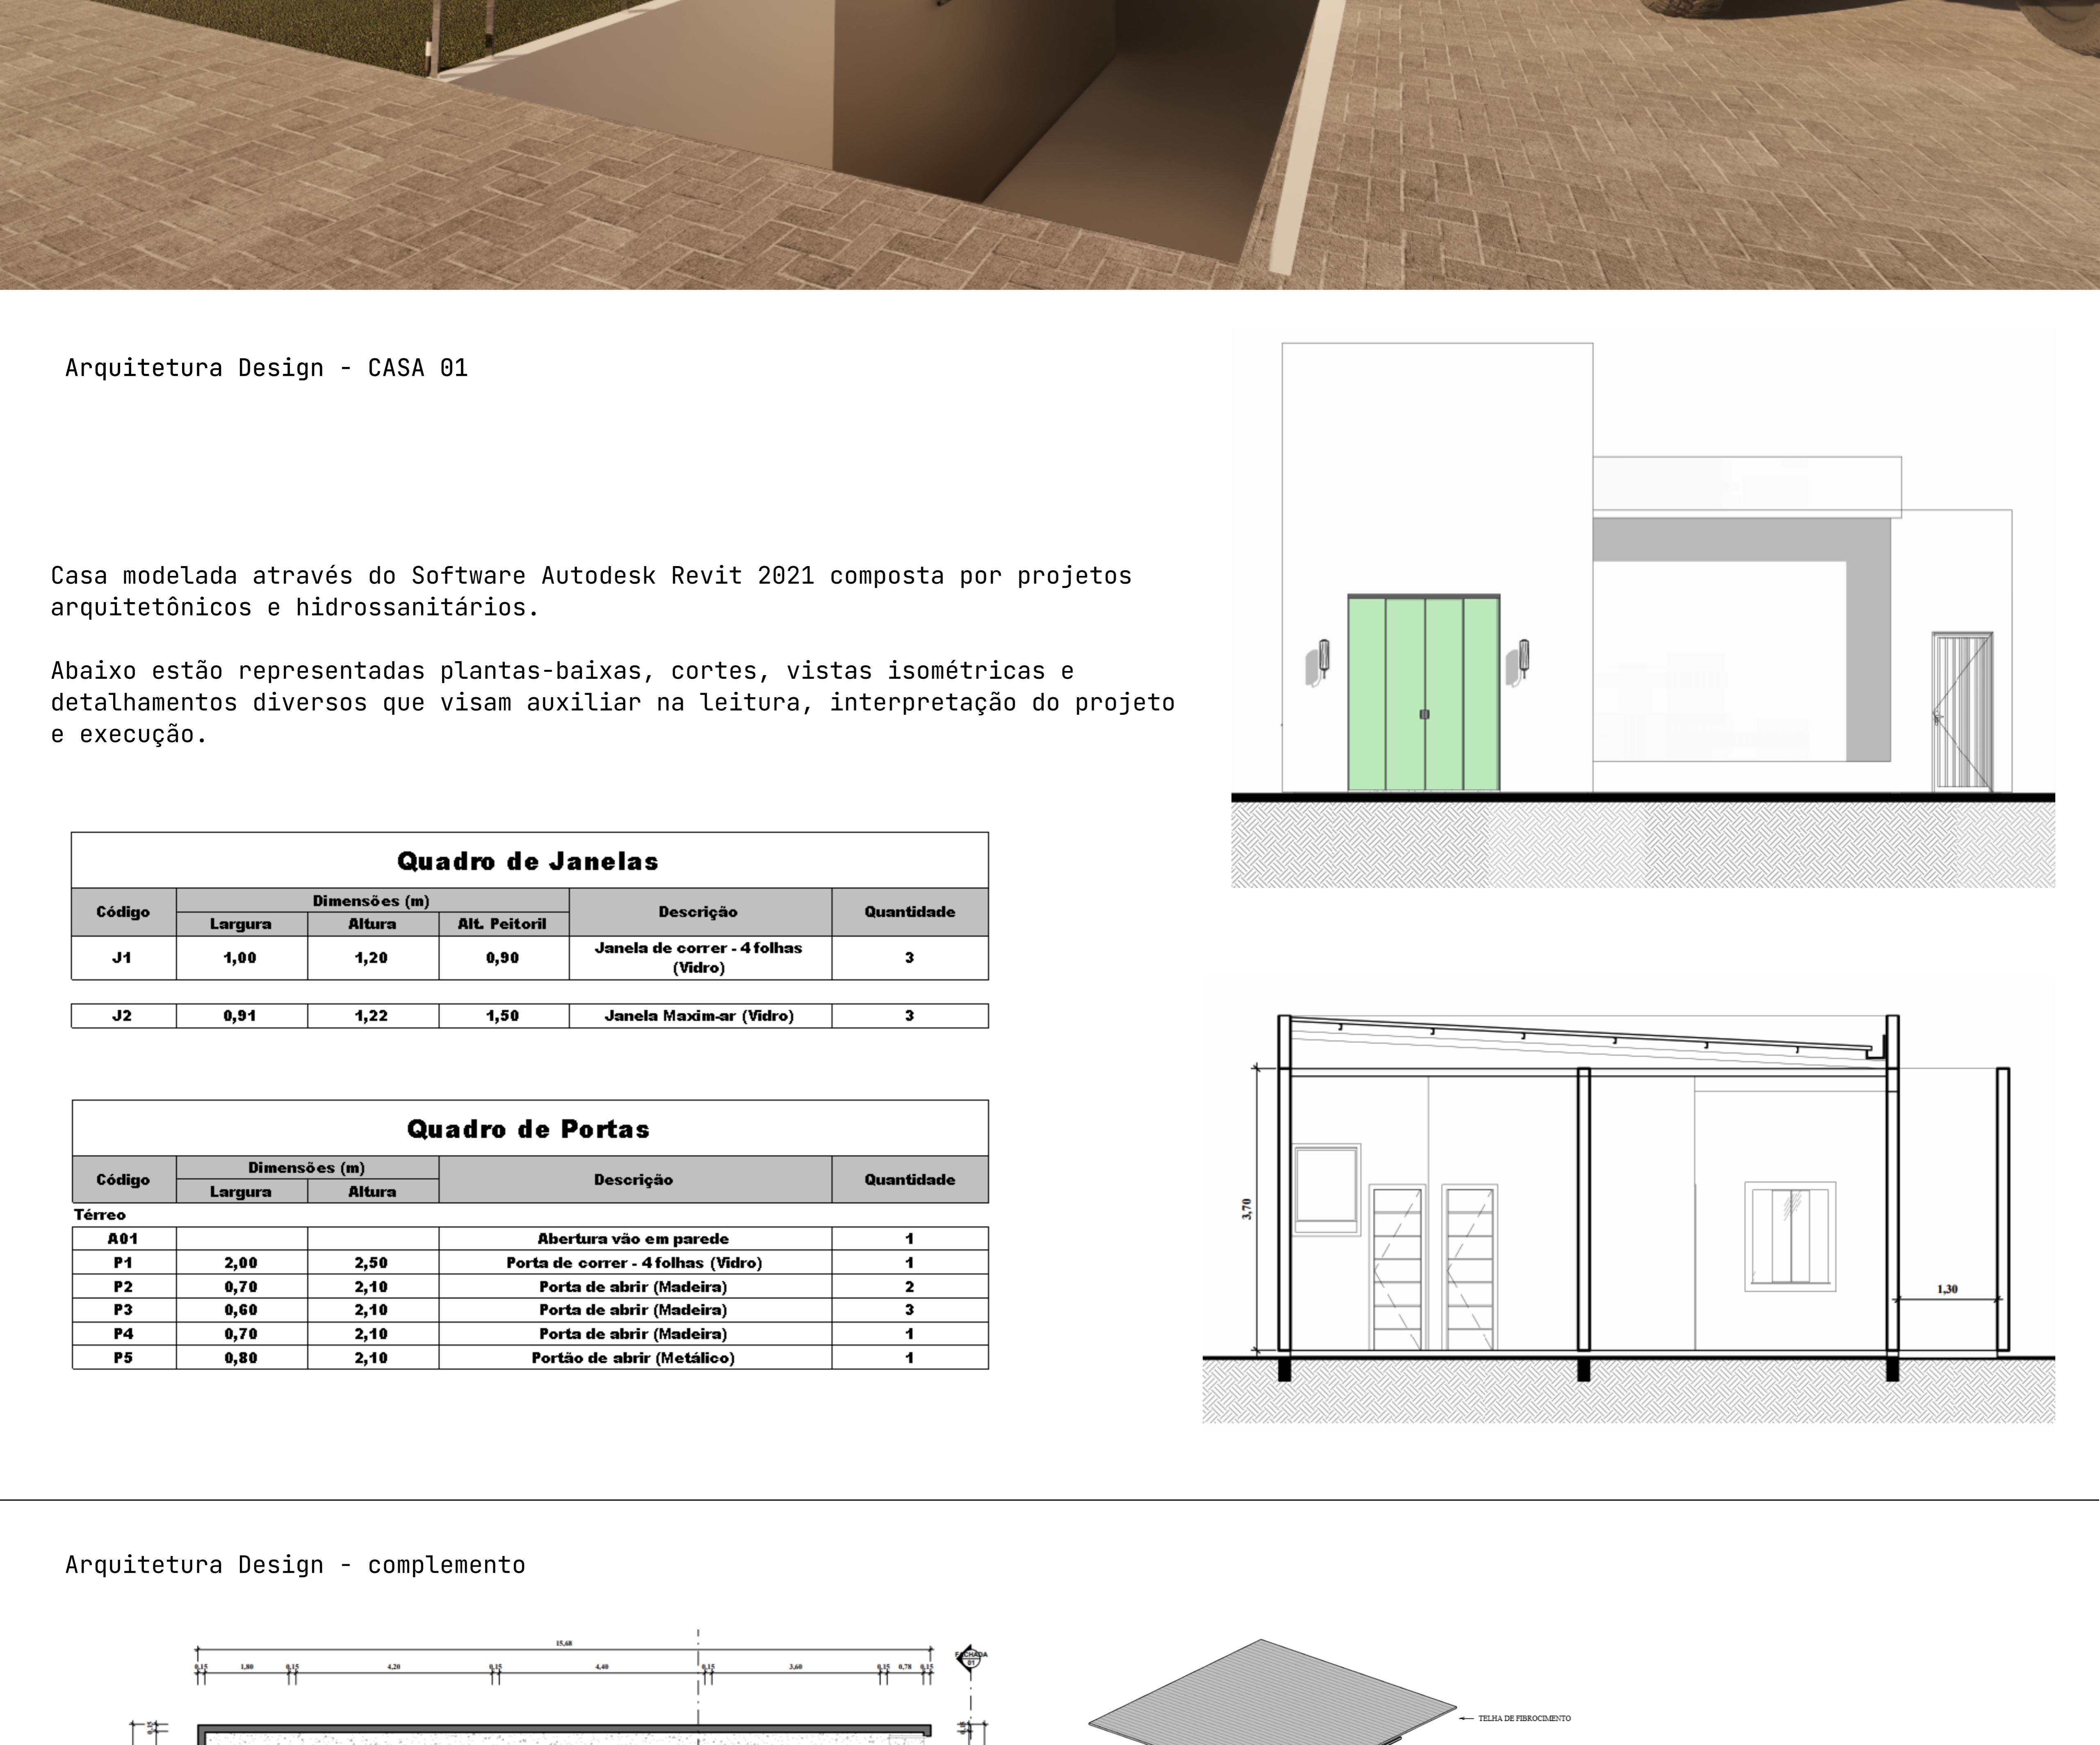


Arquitetura Design - CASA 01

Casa modelada através do Software Autodesk Revit 2021 composta por projetos arquitetônicos e hidrossanitários.



Abaixo estão representadas plantas-baixas, cortes, vistas isométricas e detalhamentos diversos que visam auxiliar na leitura, interpretação do projeto e execução.

Quadro de Janelas				
Código	Dimensões (m)		Descrição	Quantidade
J1	Largura 1,00 Altura 1,20 Alt. Peitoril 0,90		Janela de correr - 4 folhas (Vidro)	3
J2	0,91 1,22 1,50		Janela Maxim-ar (Vidro)	3



Quadro de Portas				
Código	Largura	Altura	Descrição	Quantidade
Térreo				
A01			Abertura viva em parede	1
P1	2,00	2,50	Porta de correr - 4 folhas (Vidro)	1
P2	0,70	2,10	Porta de abrir (Madeira)	2
P3	0,60	2,10	Porta de abrir (Madeira)	3
P4	0,70	2,10	Porta de abrir (Madeira)	1
P5	0,80	2,10	Portão de abrir (Metálico)	1

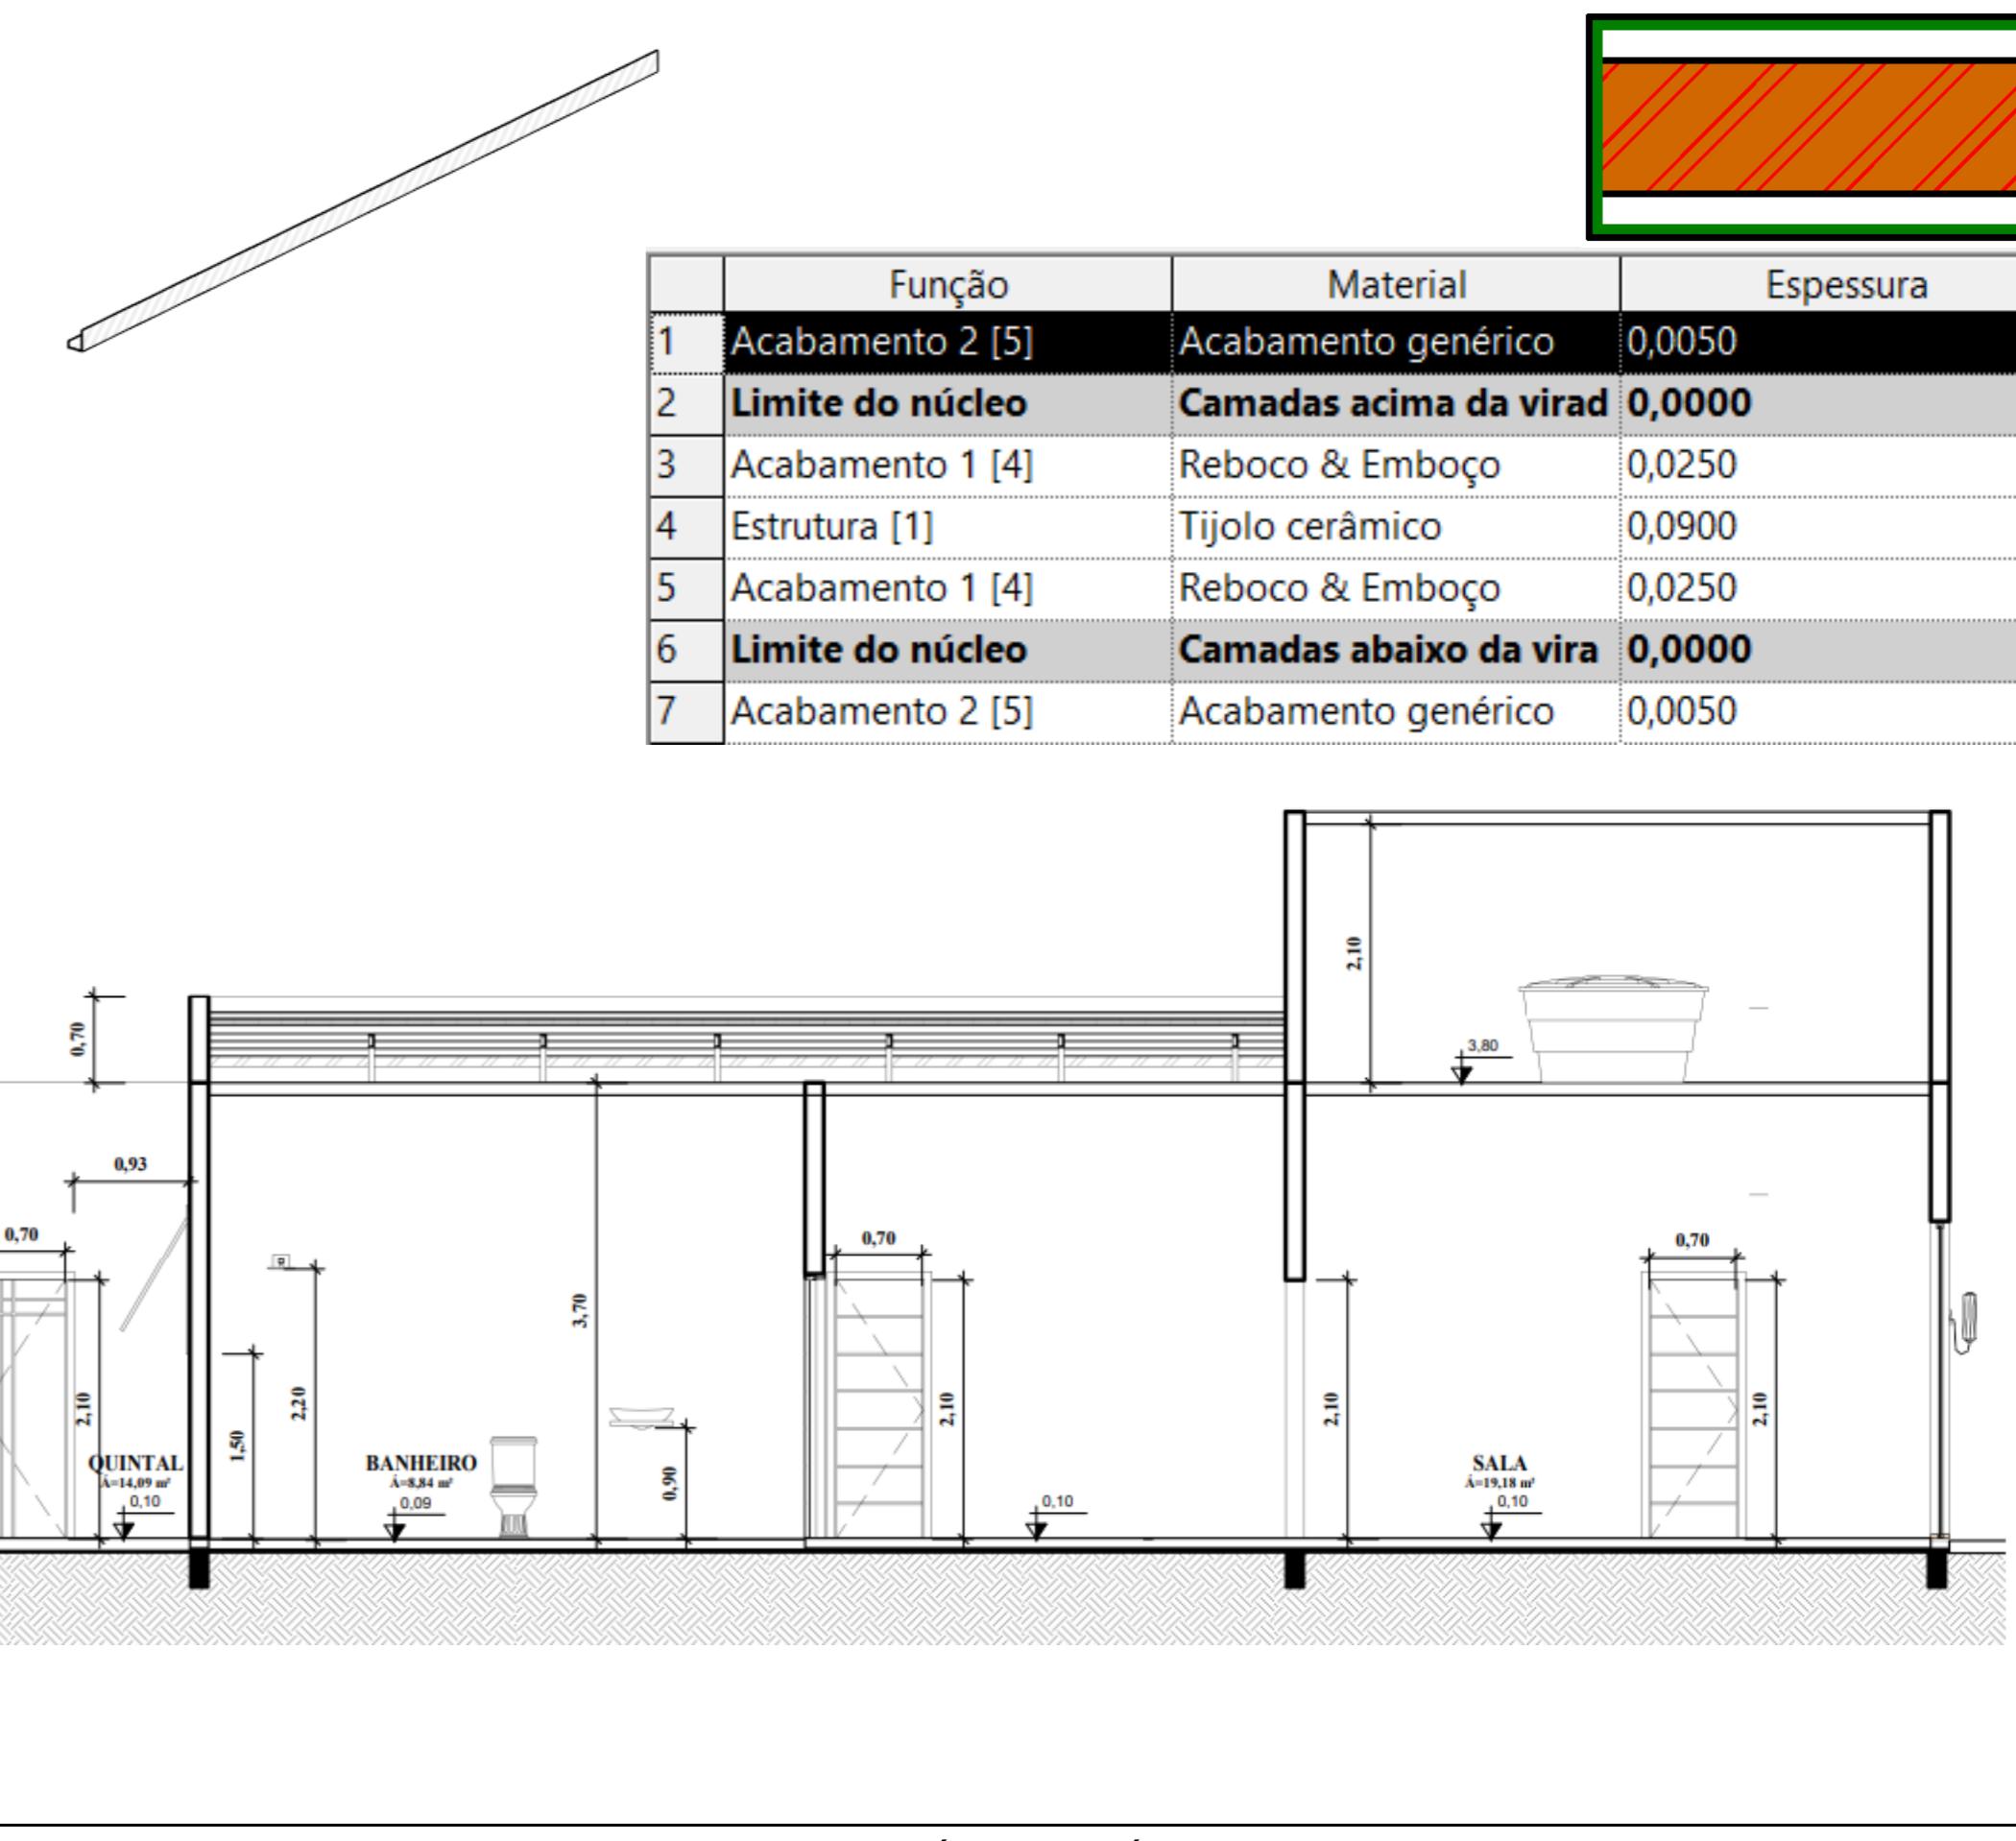



Arquitetura Design - complemento

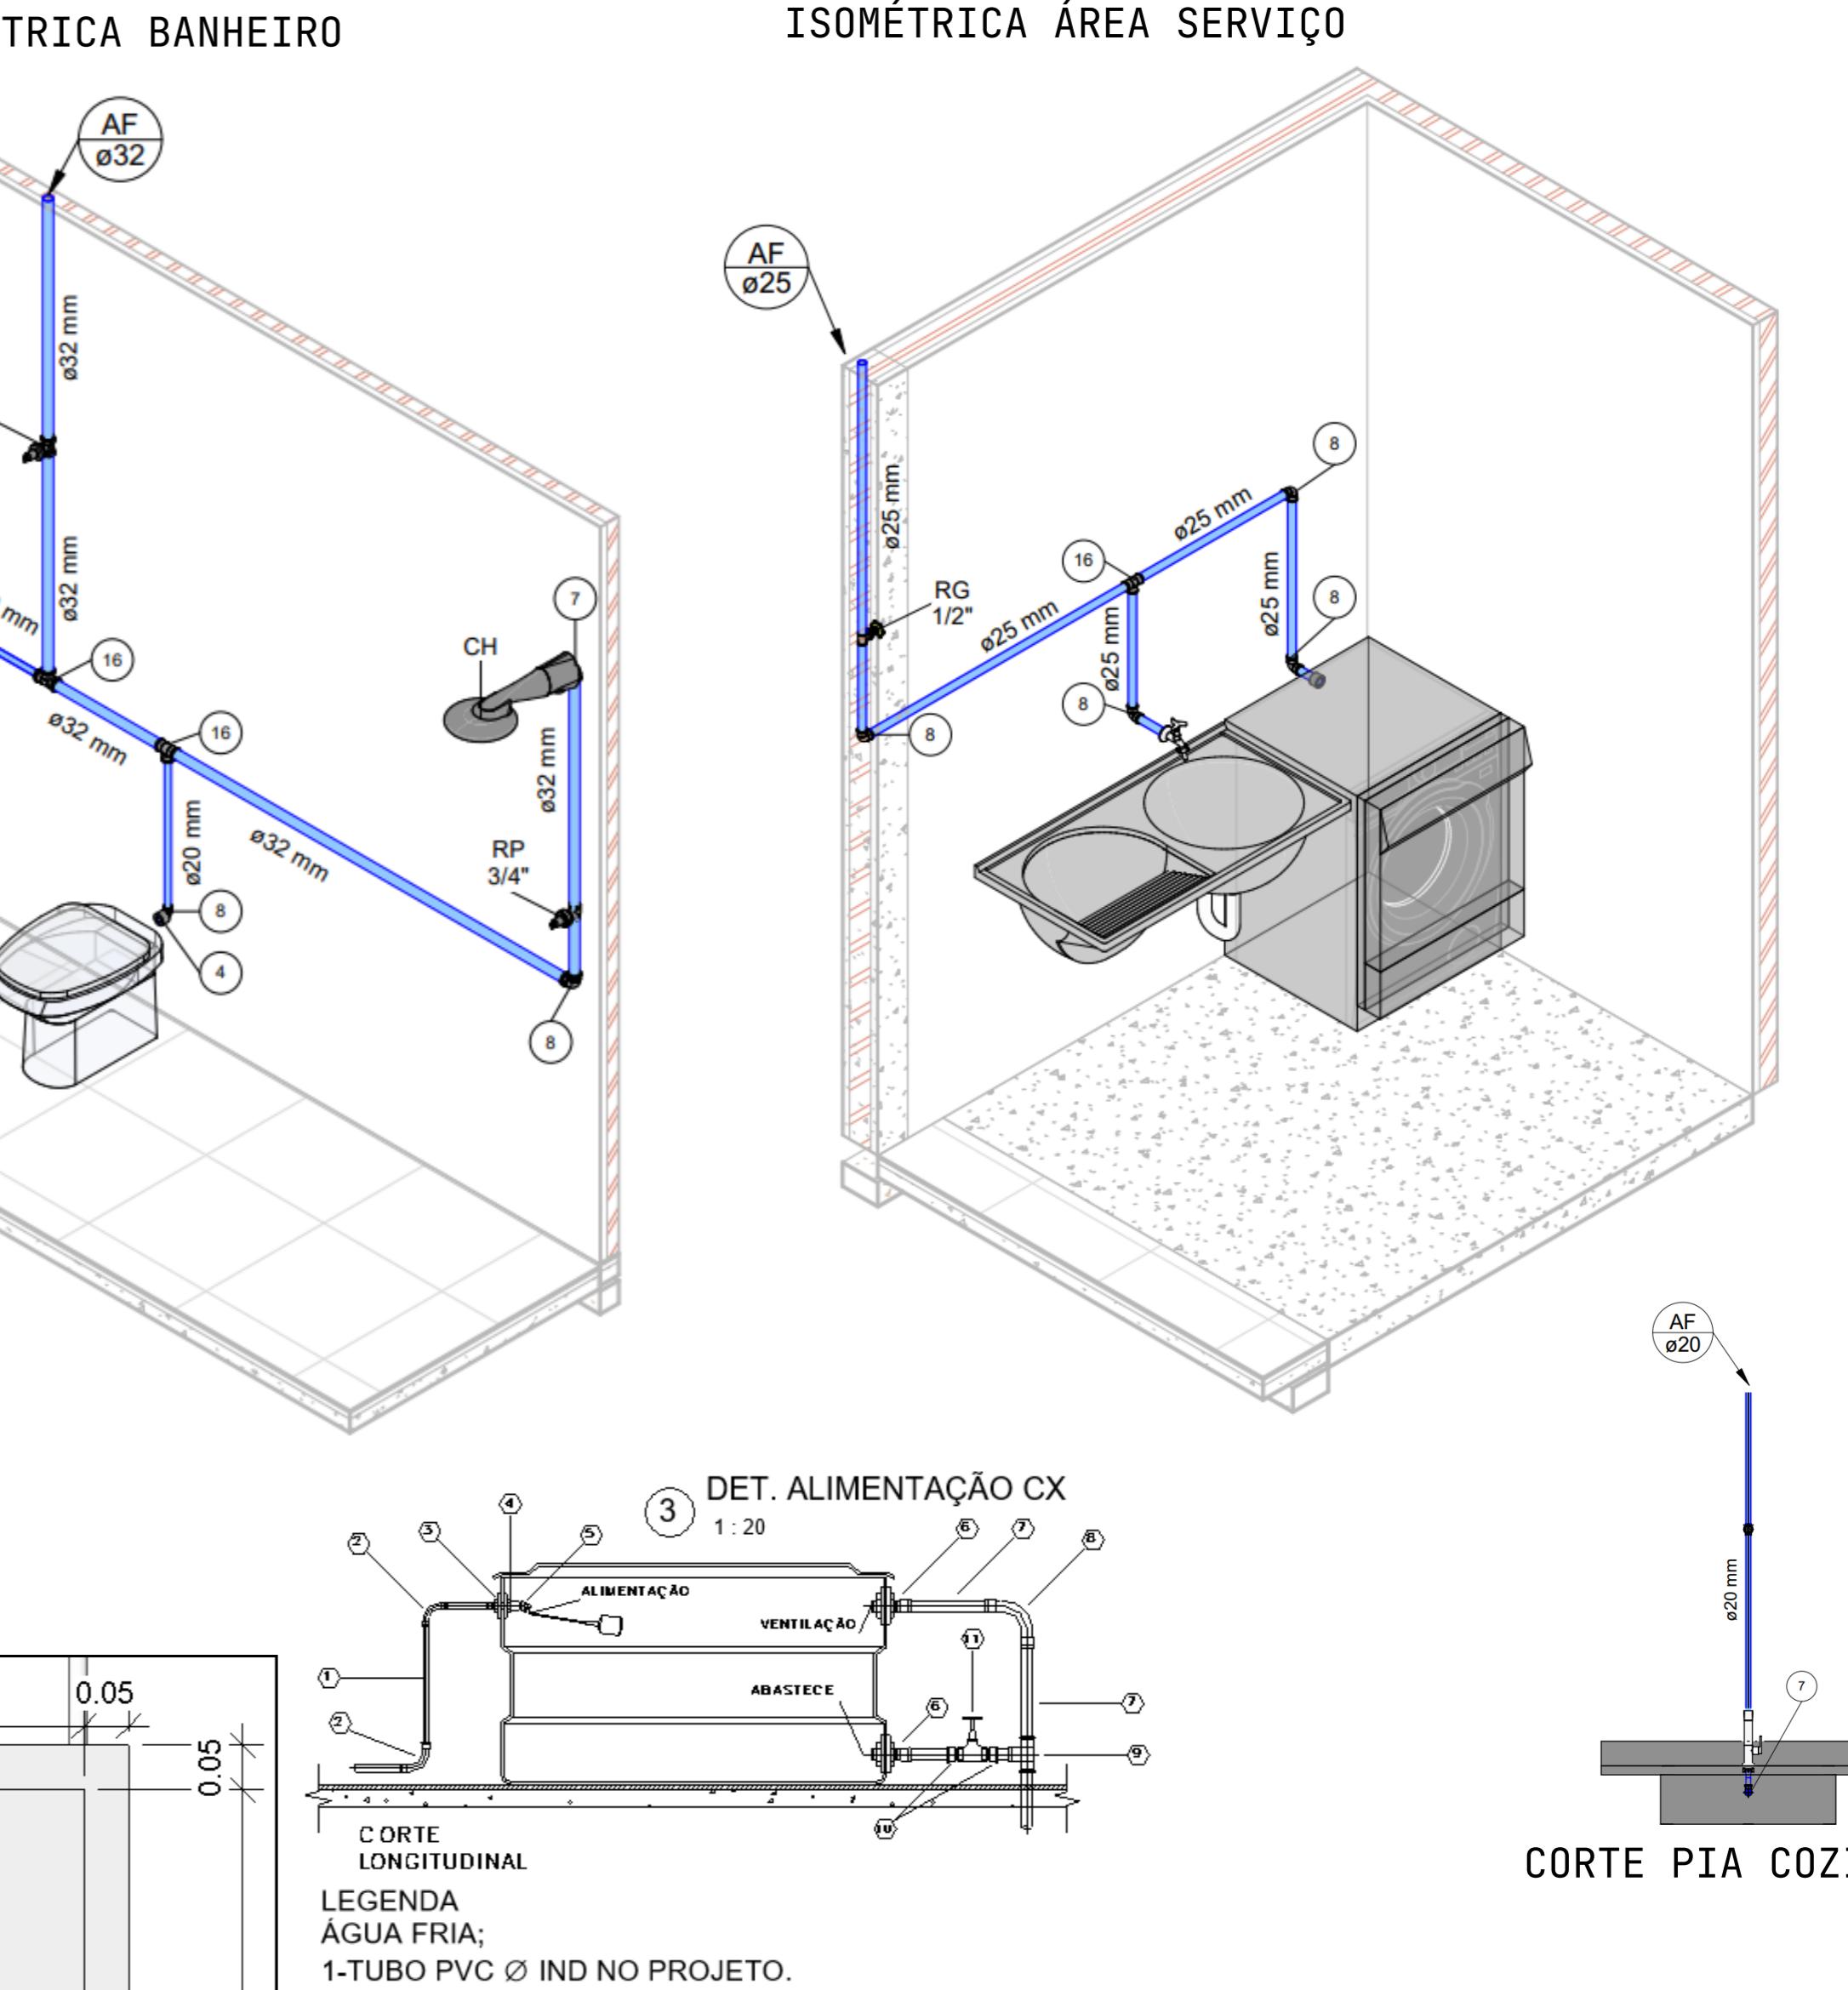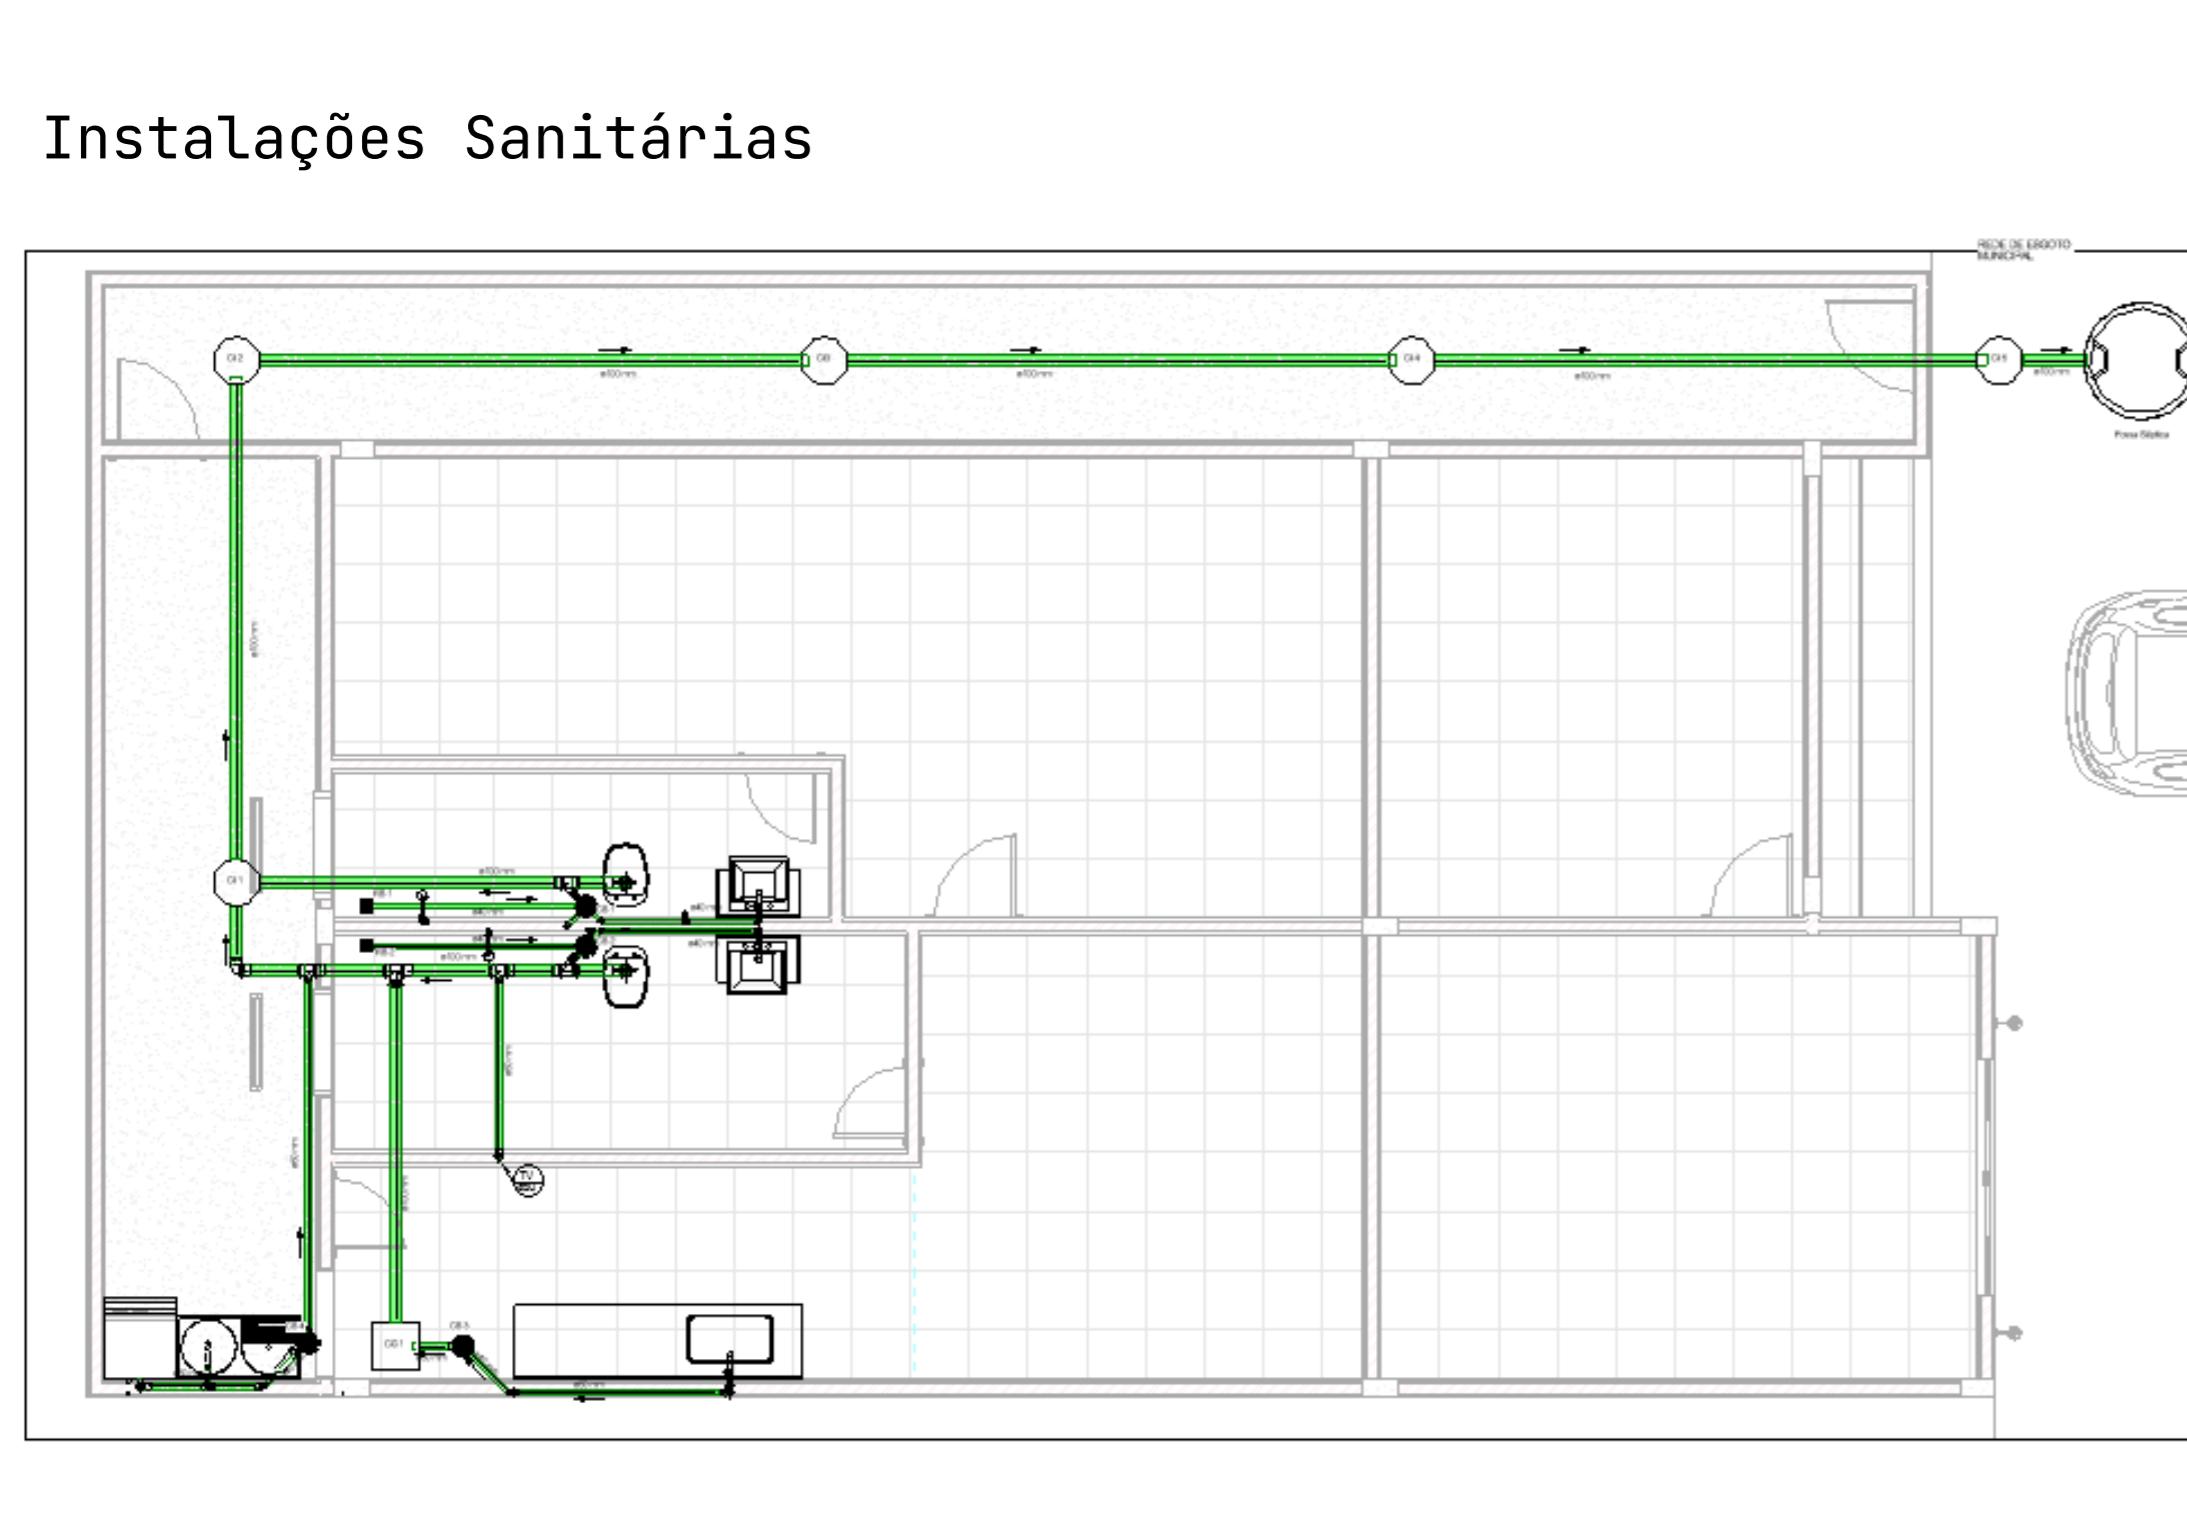



INSTALAÇÕES HIDRÁULICAS

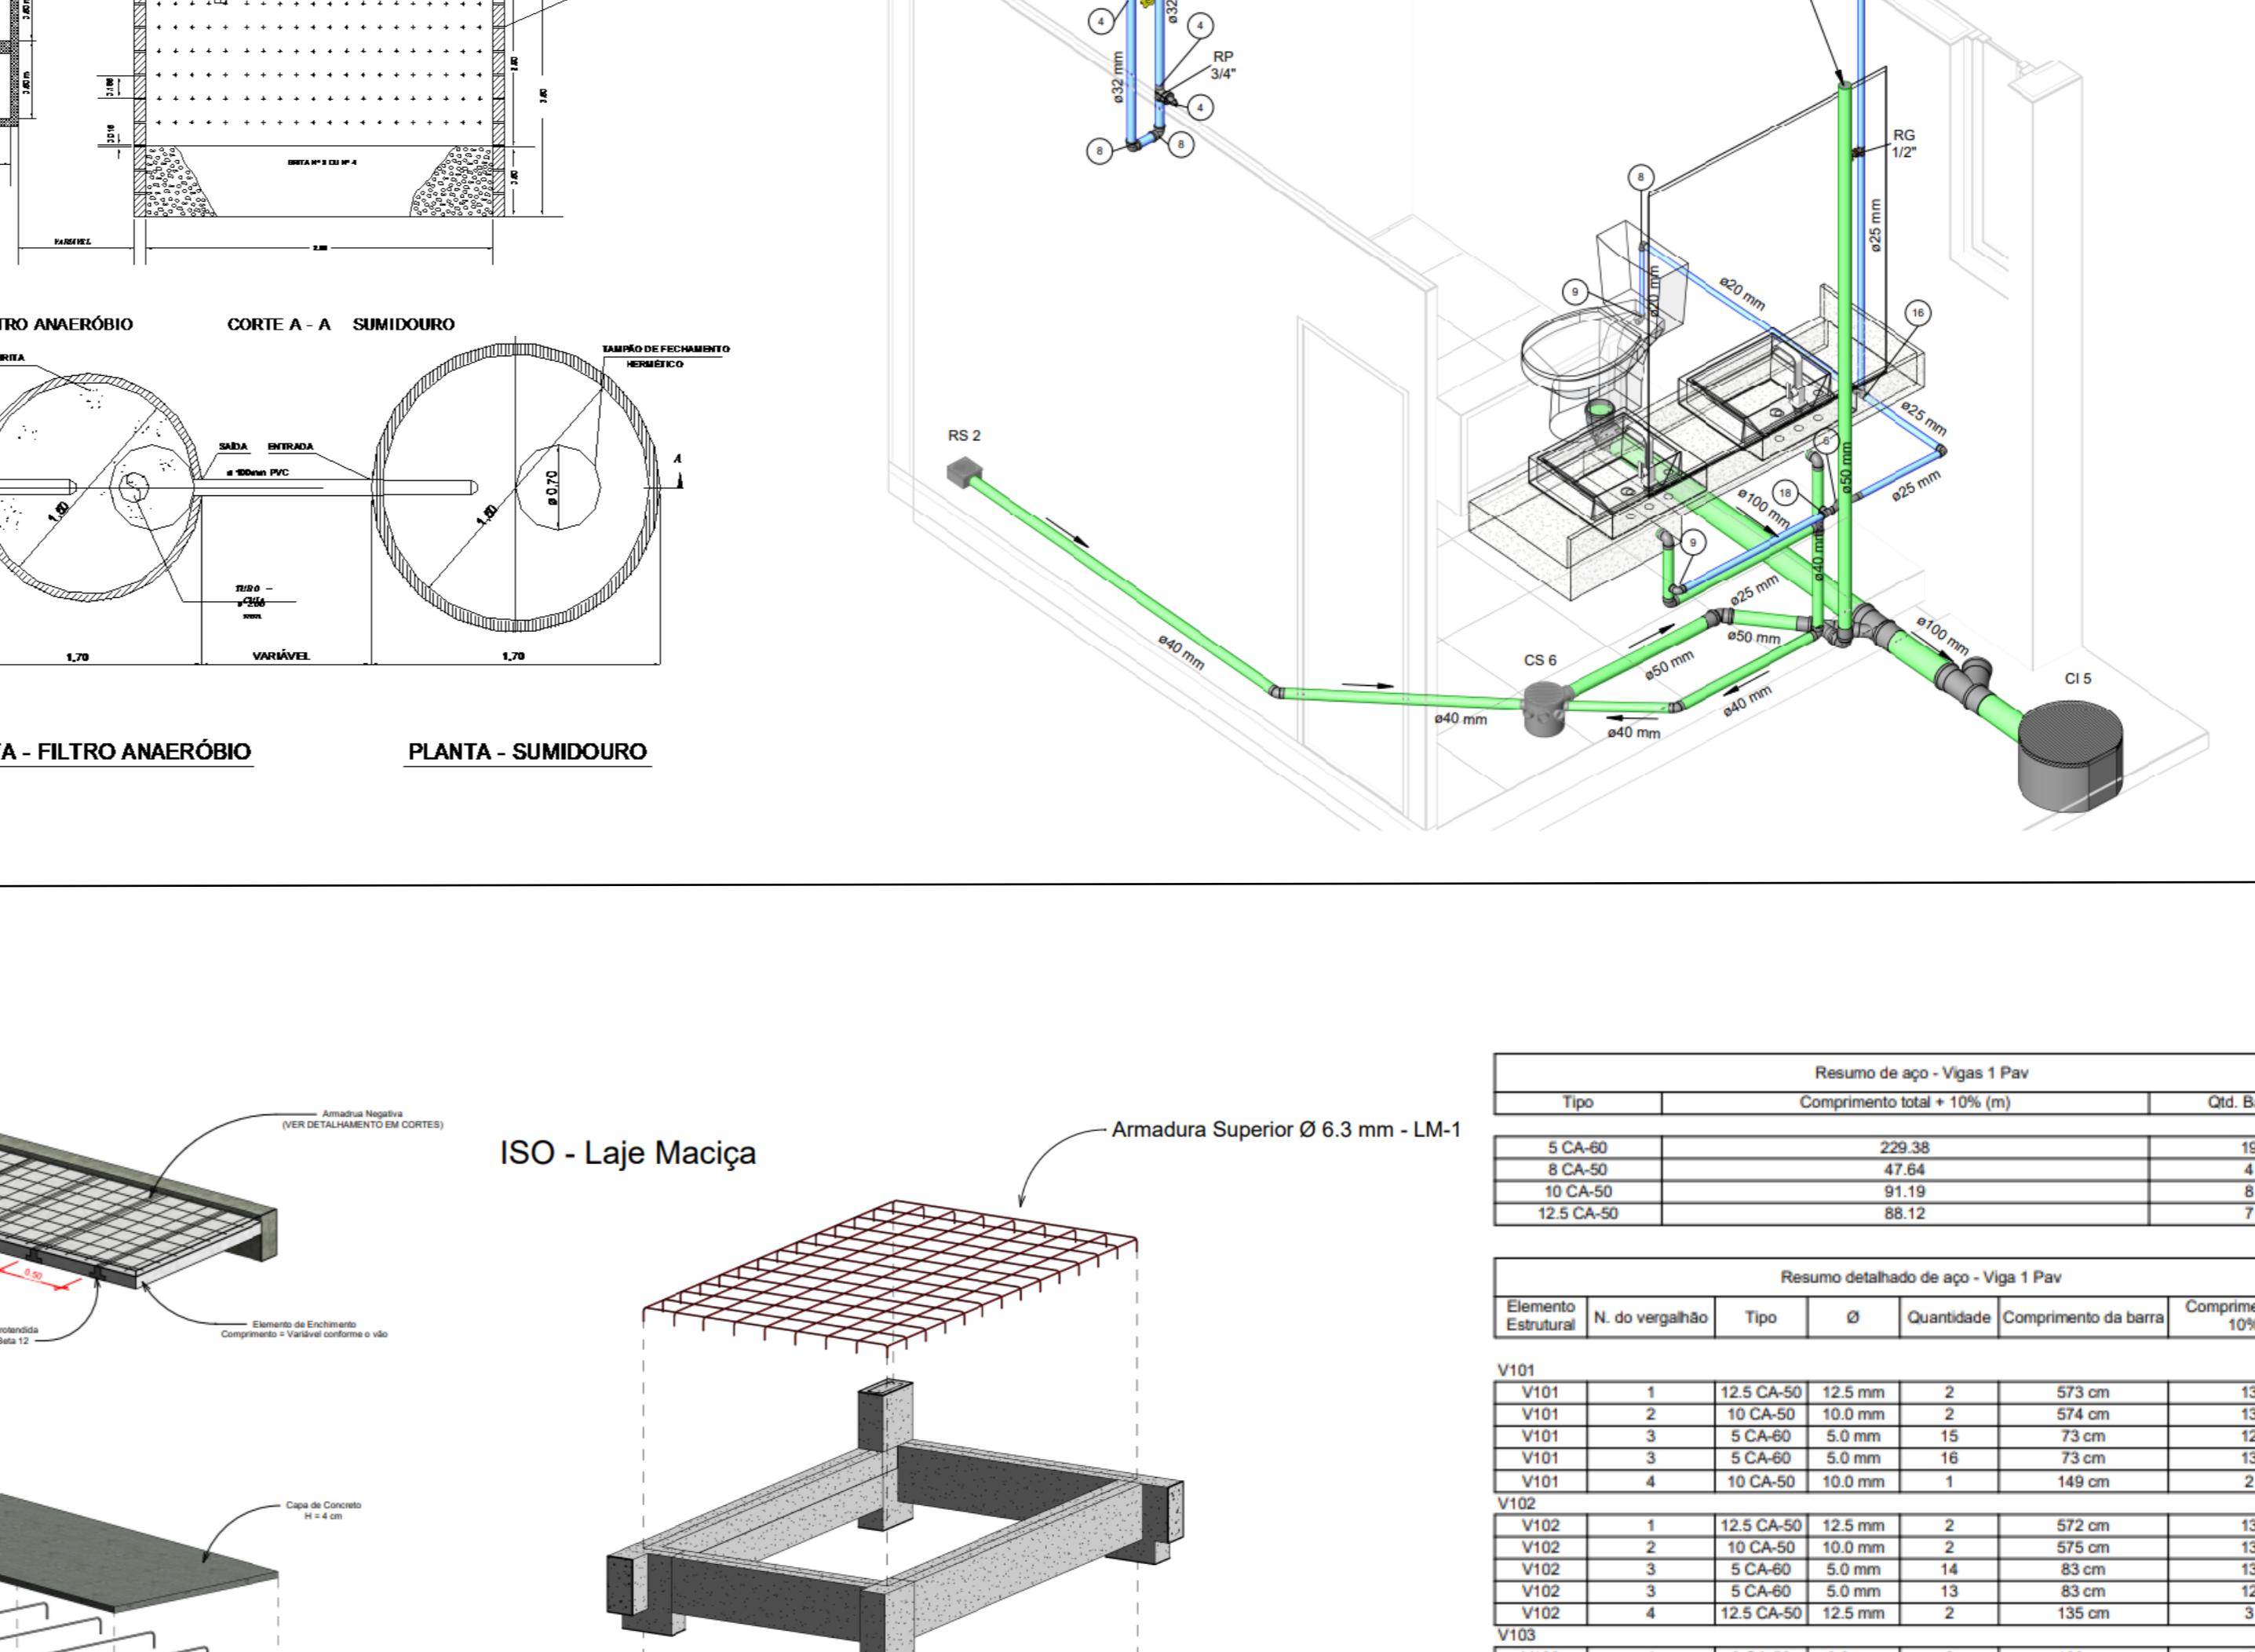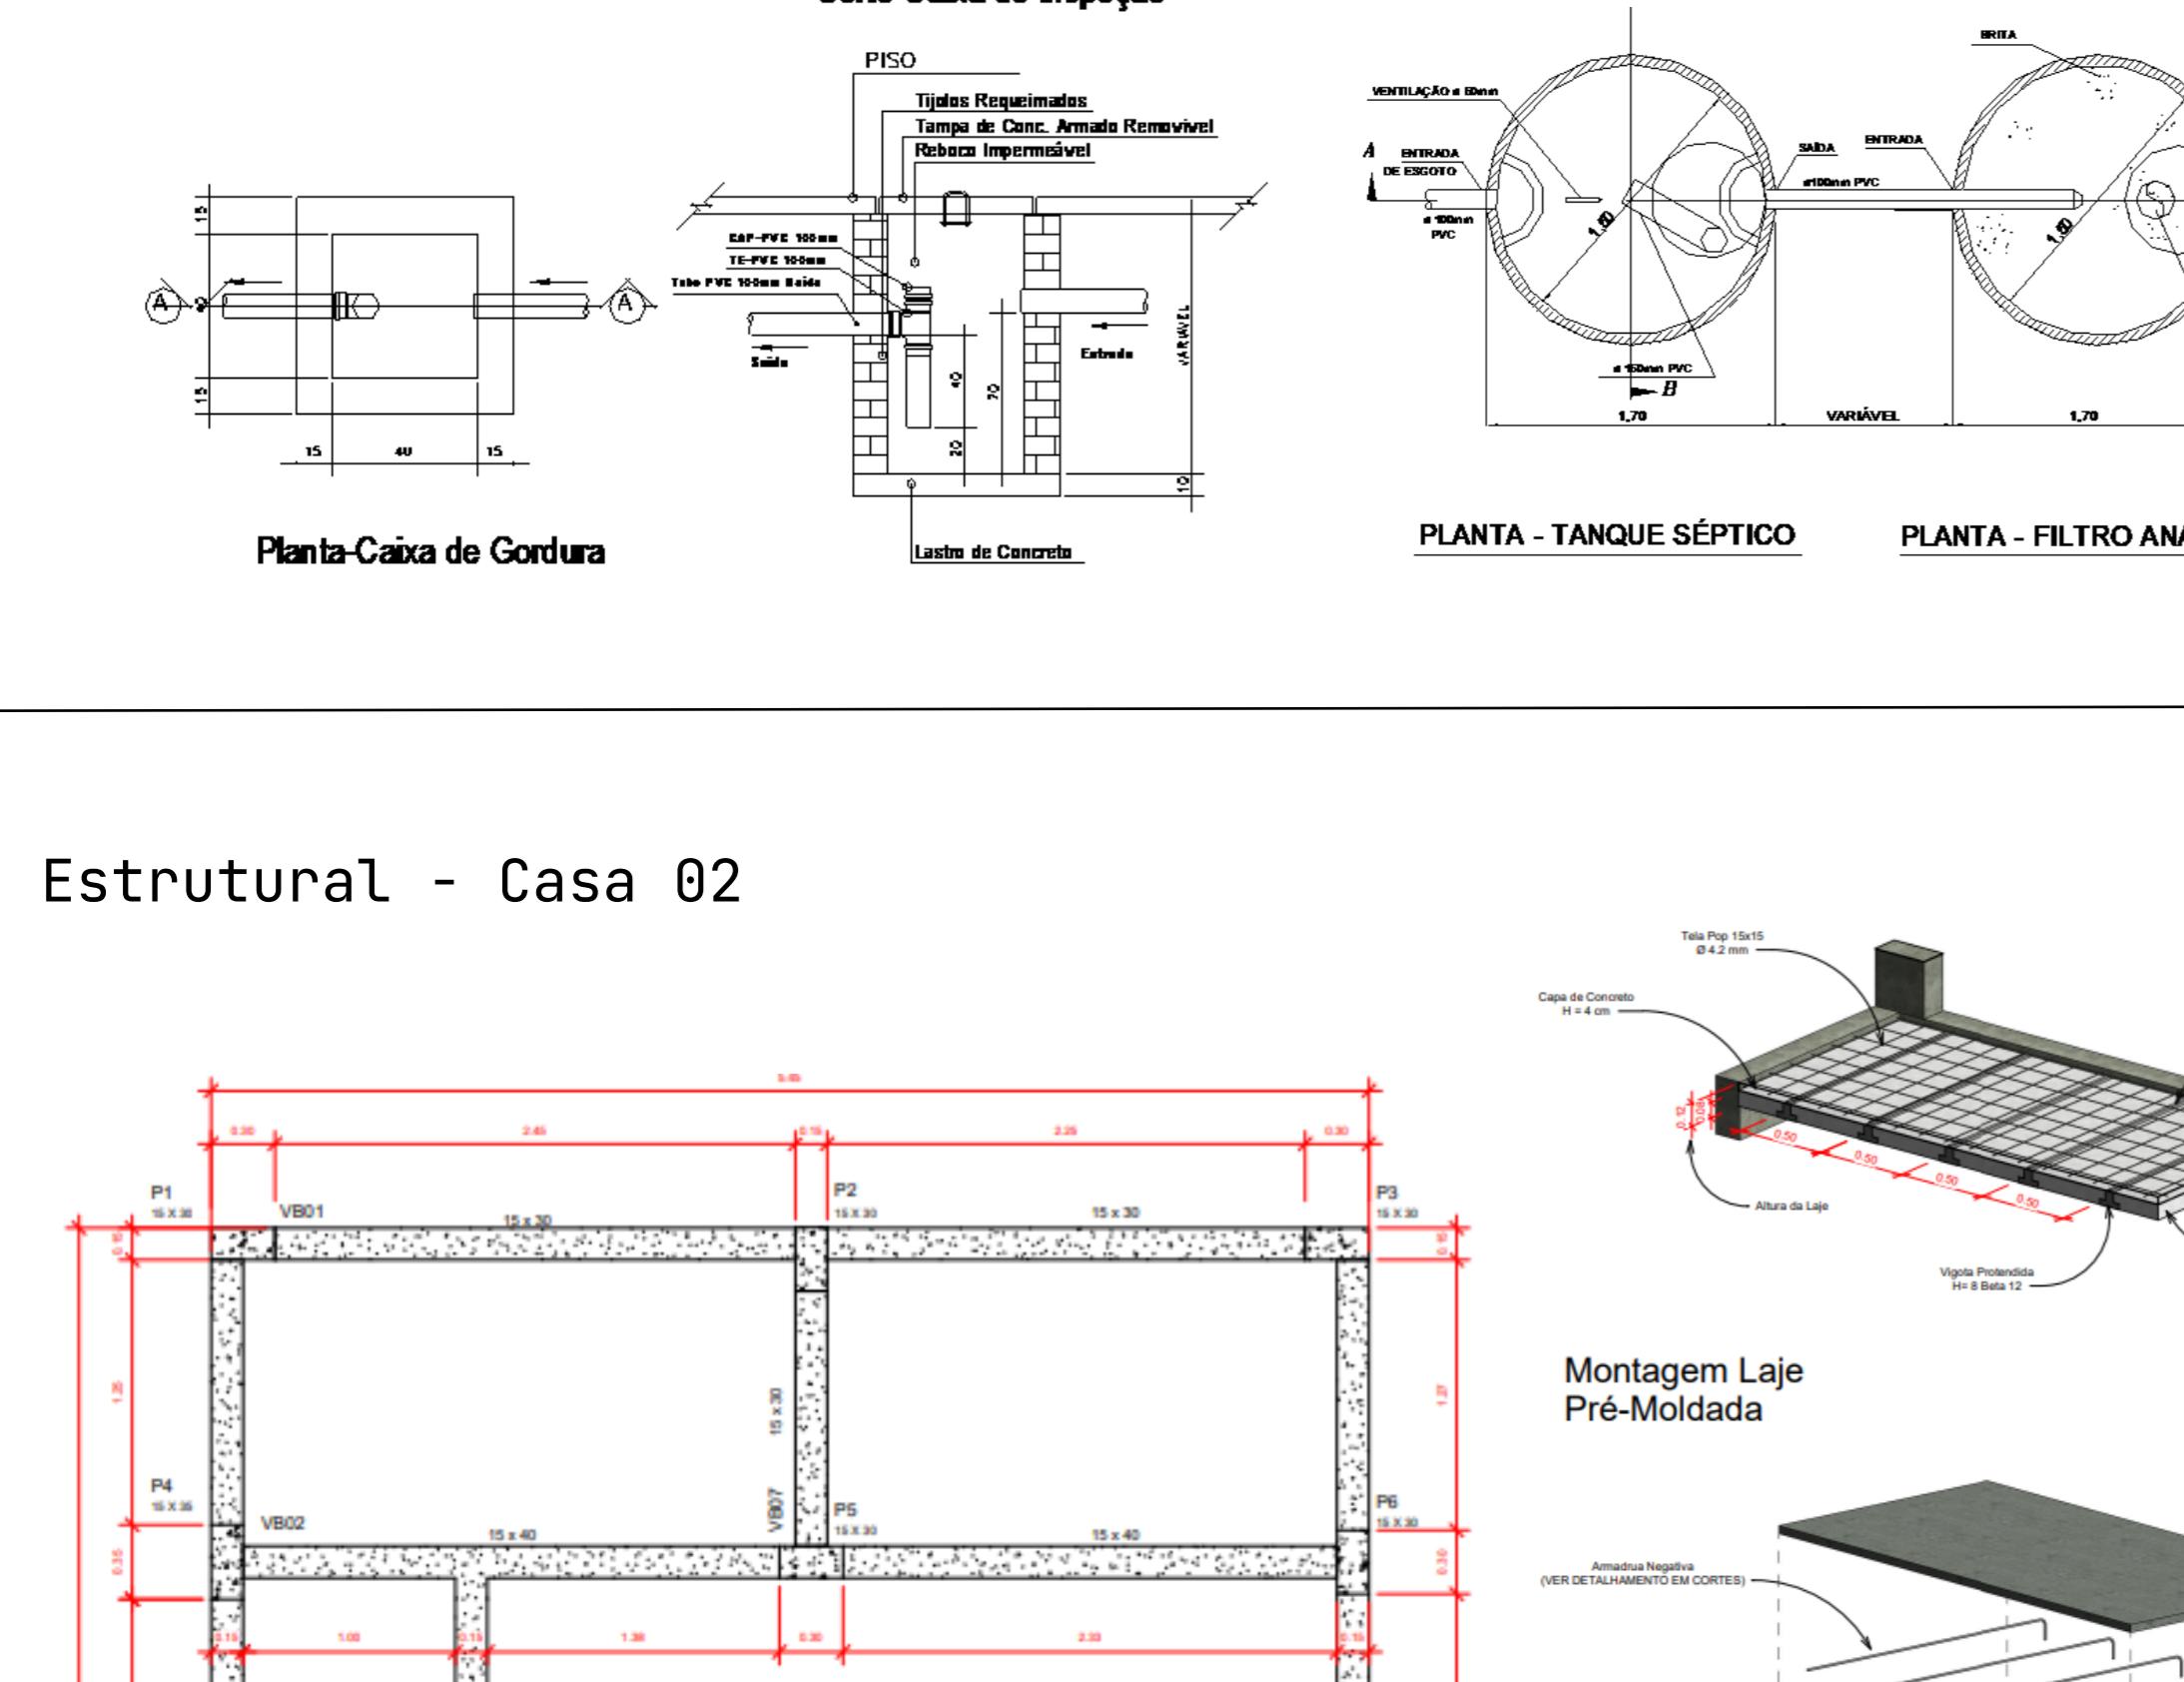

Instalações Sanitárias

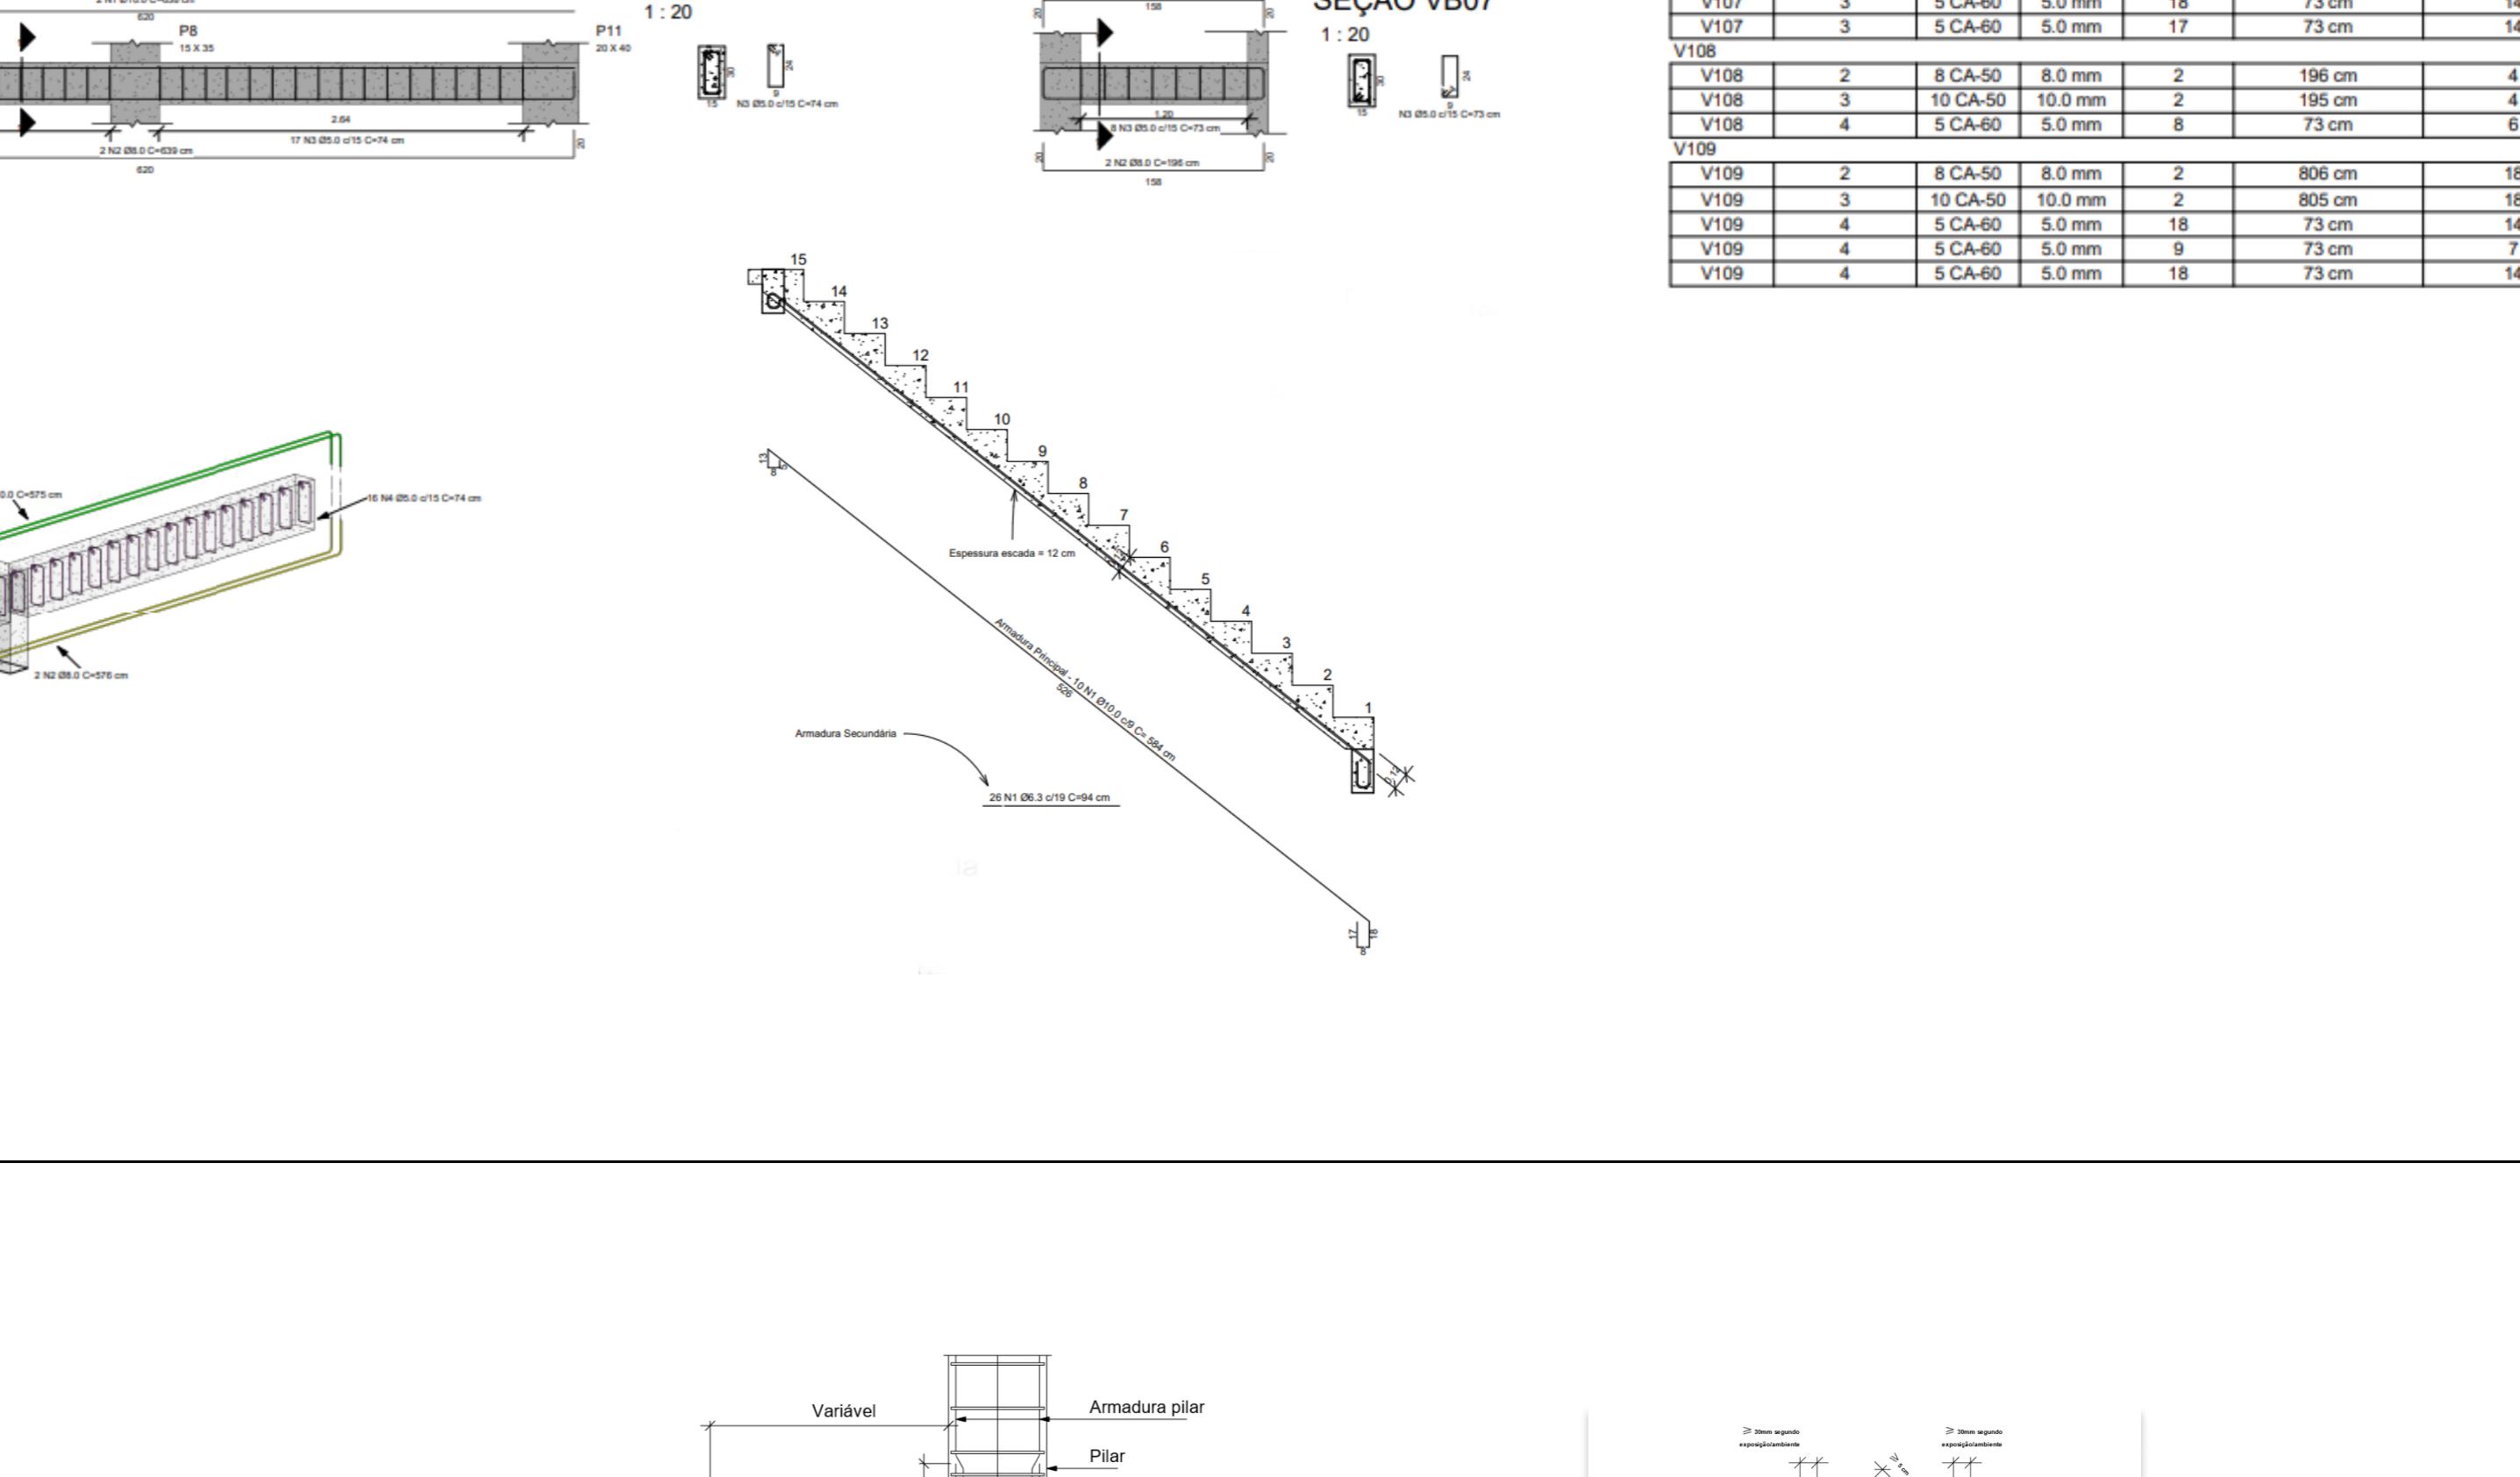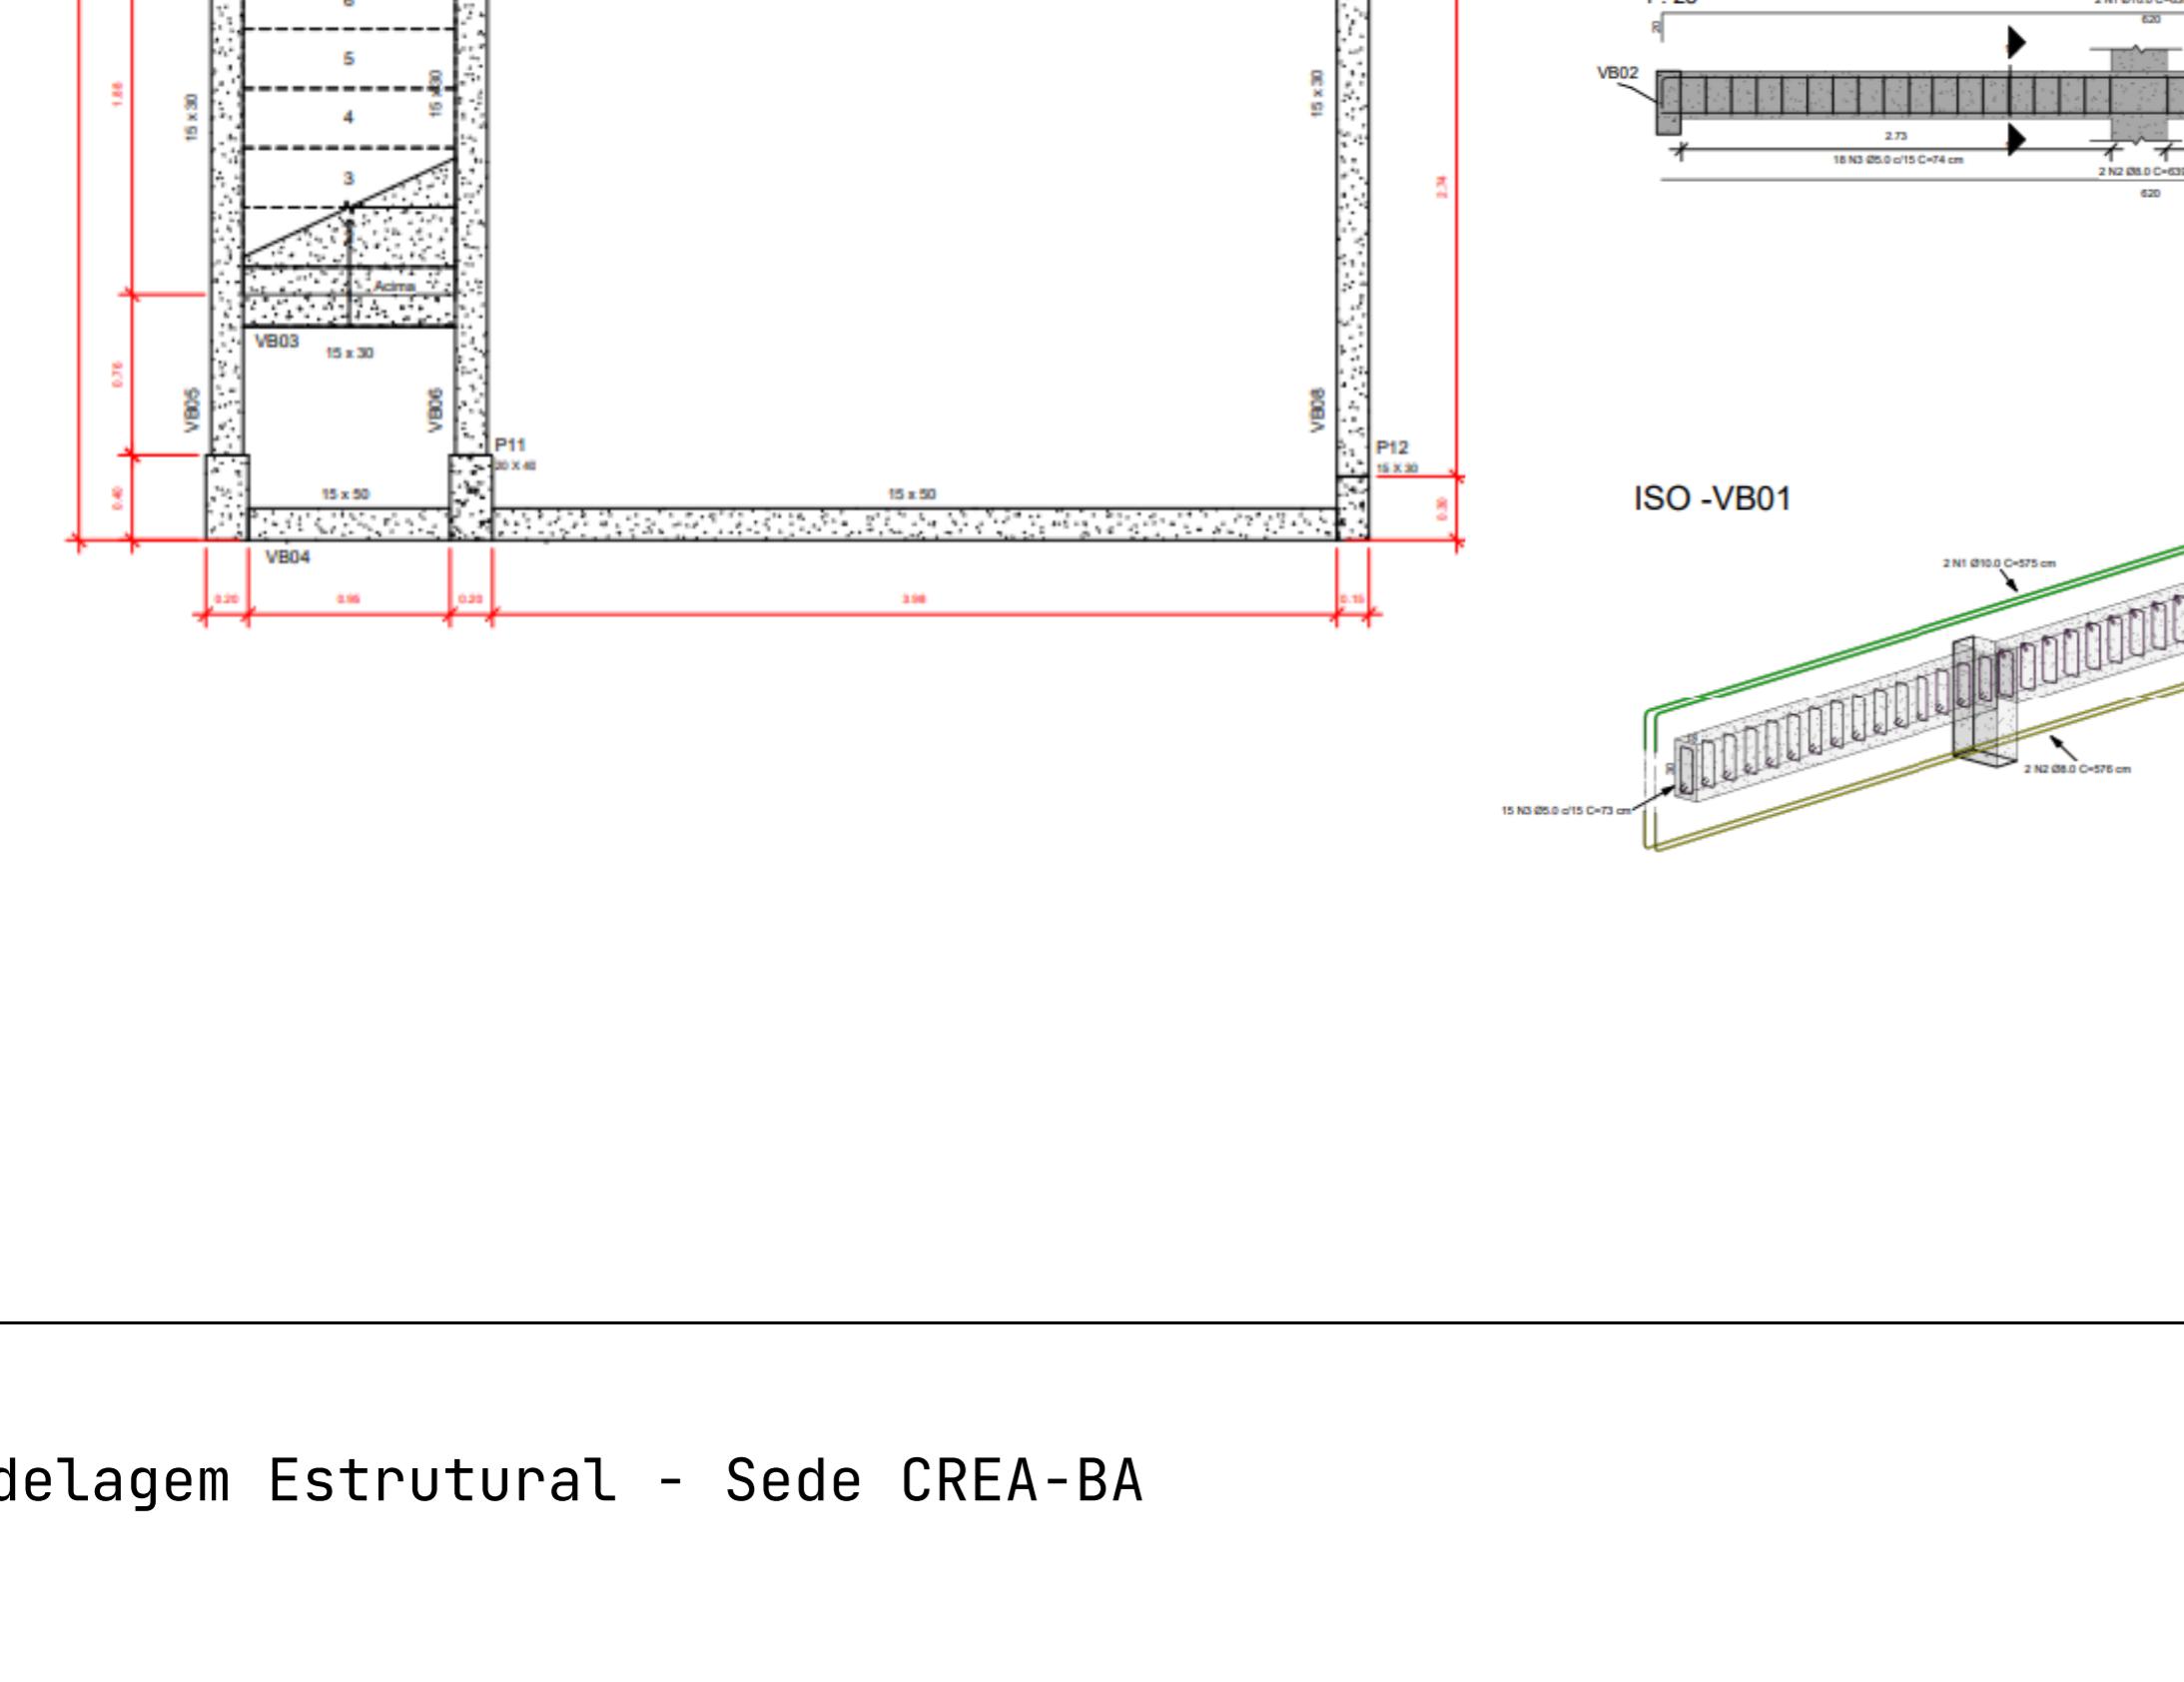

Estrutural - Casa 02

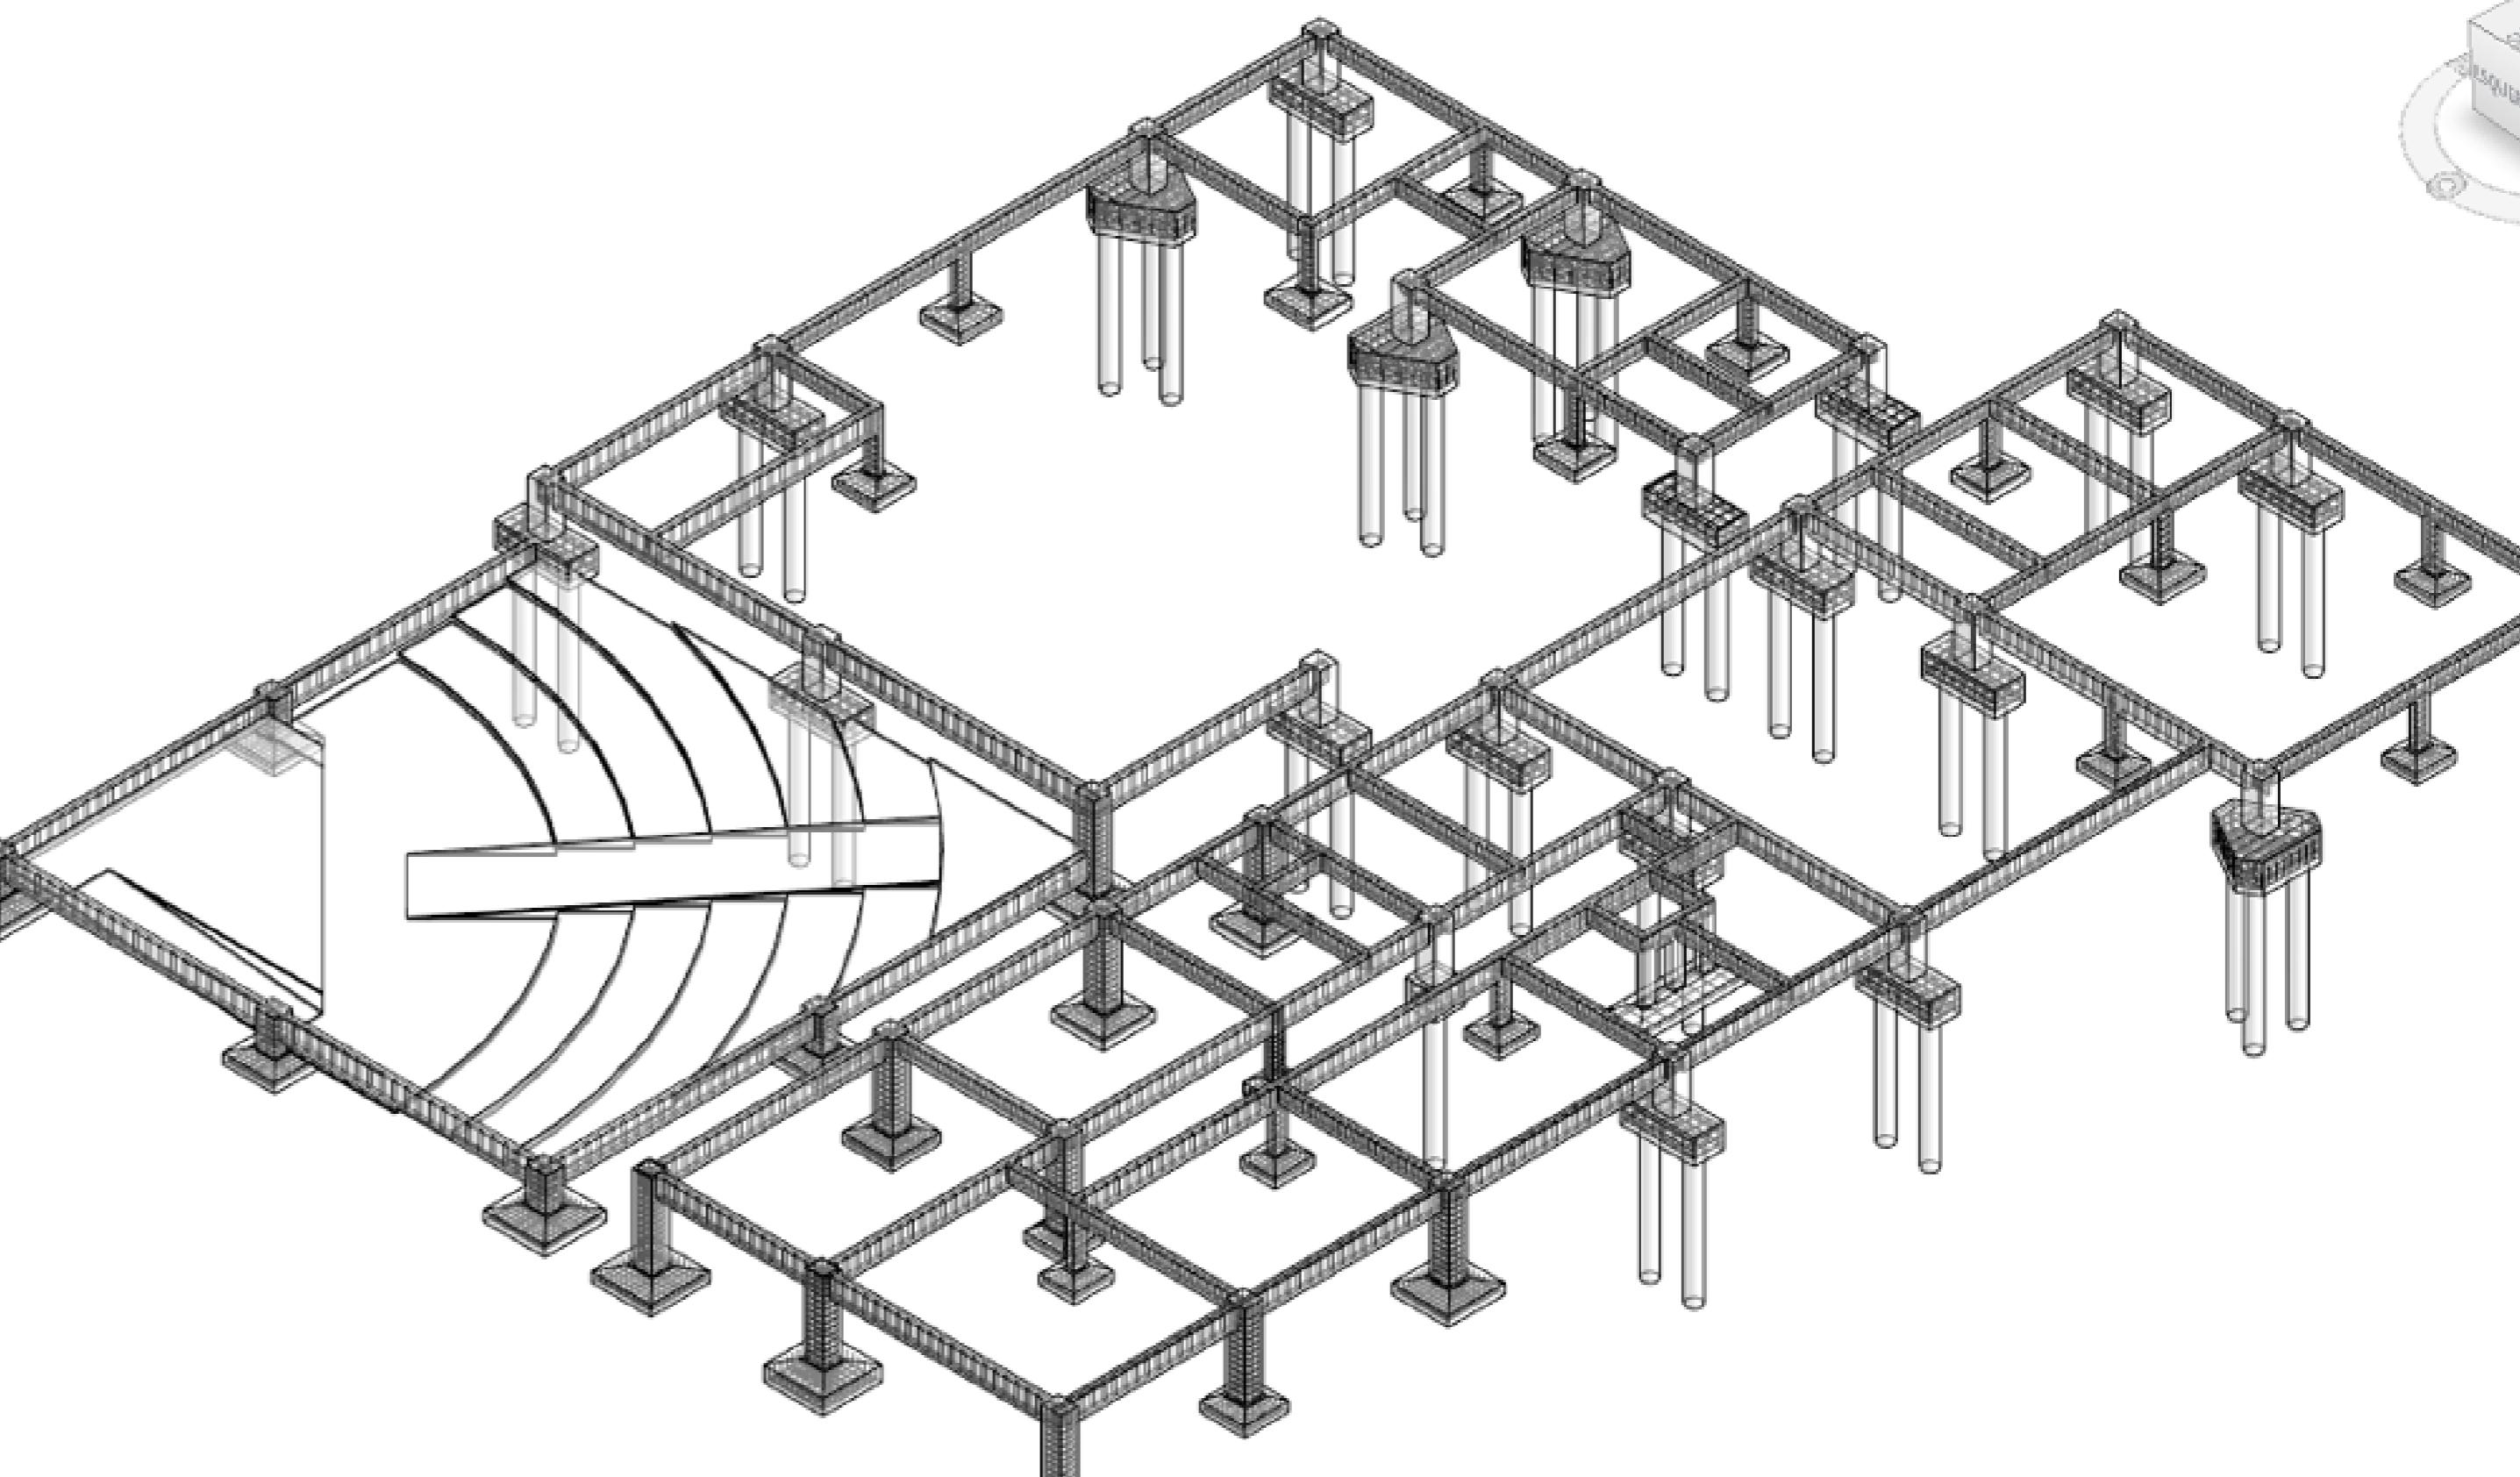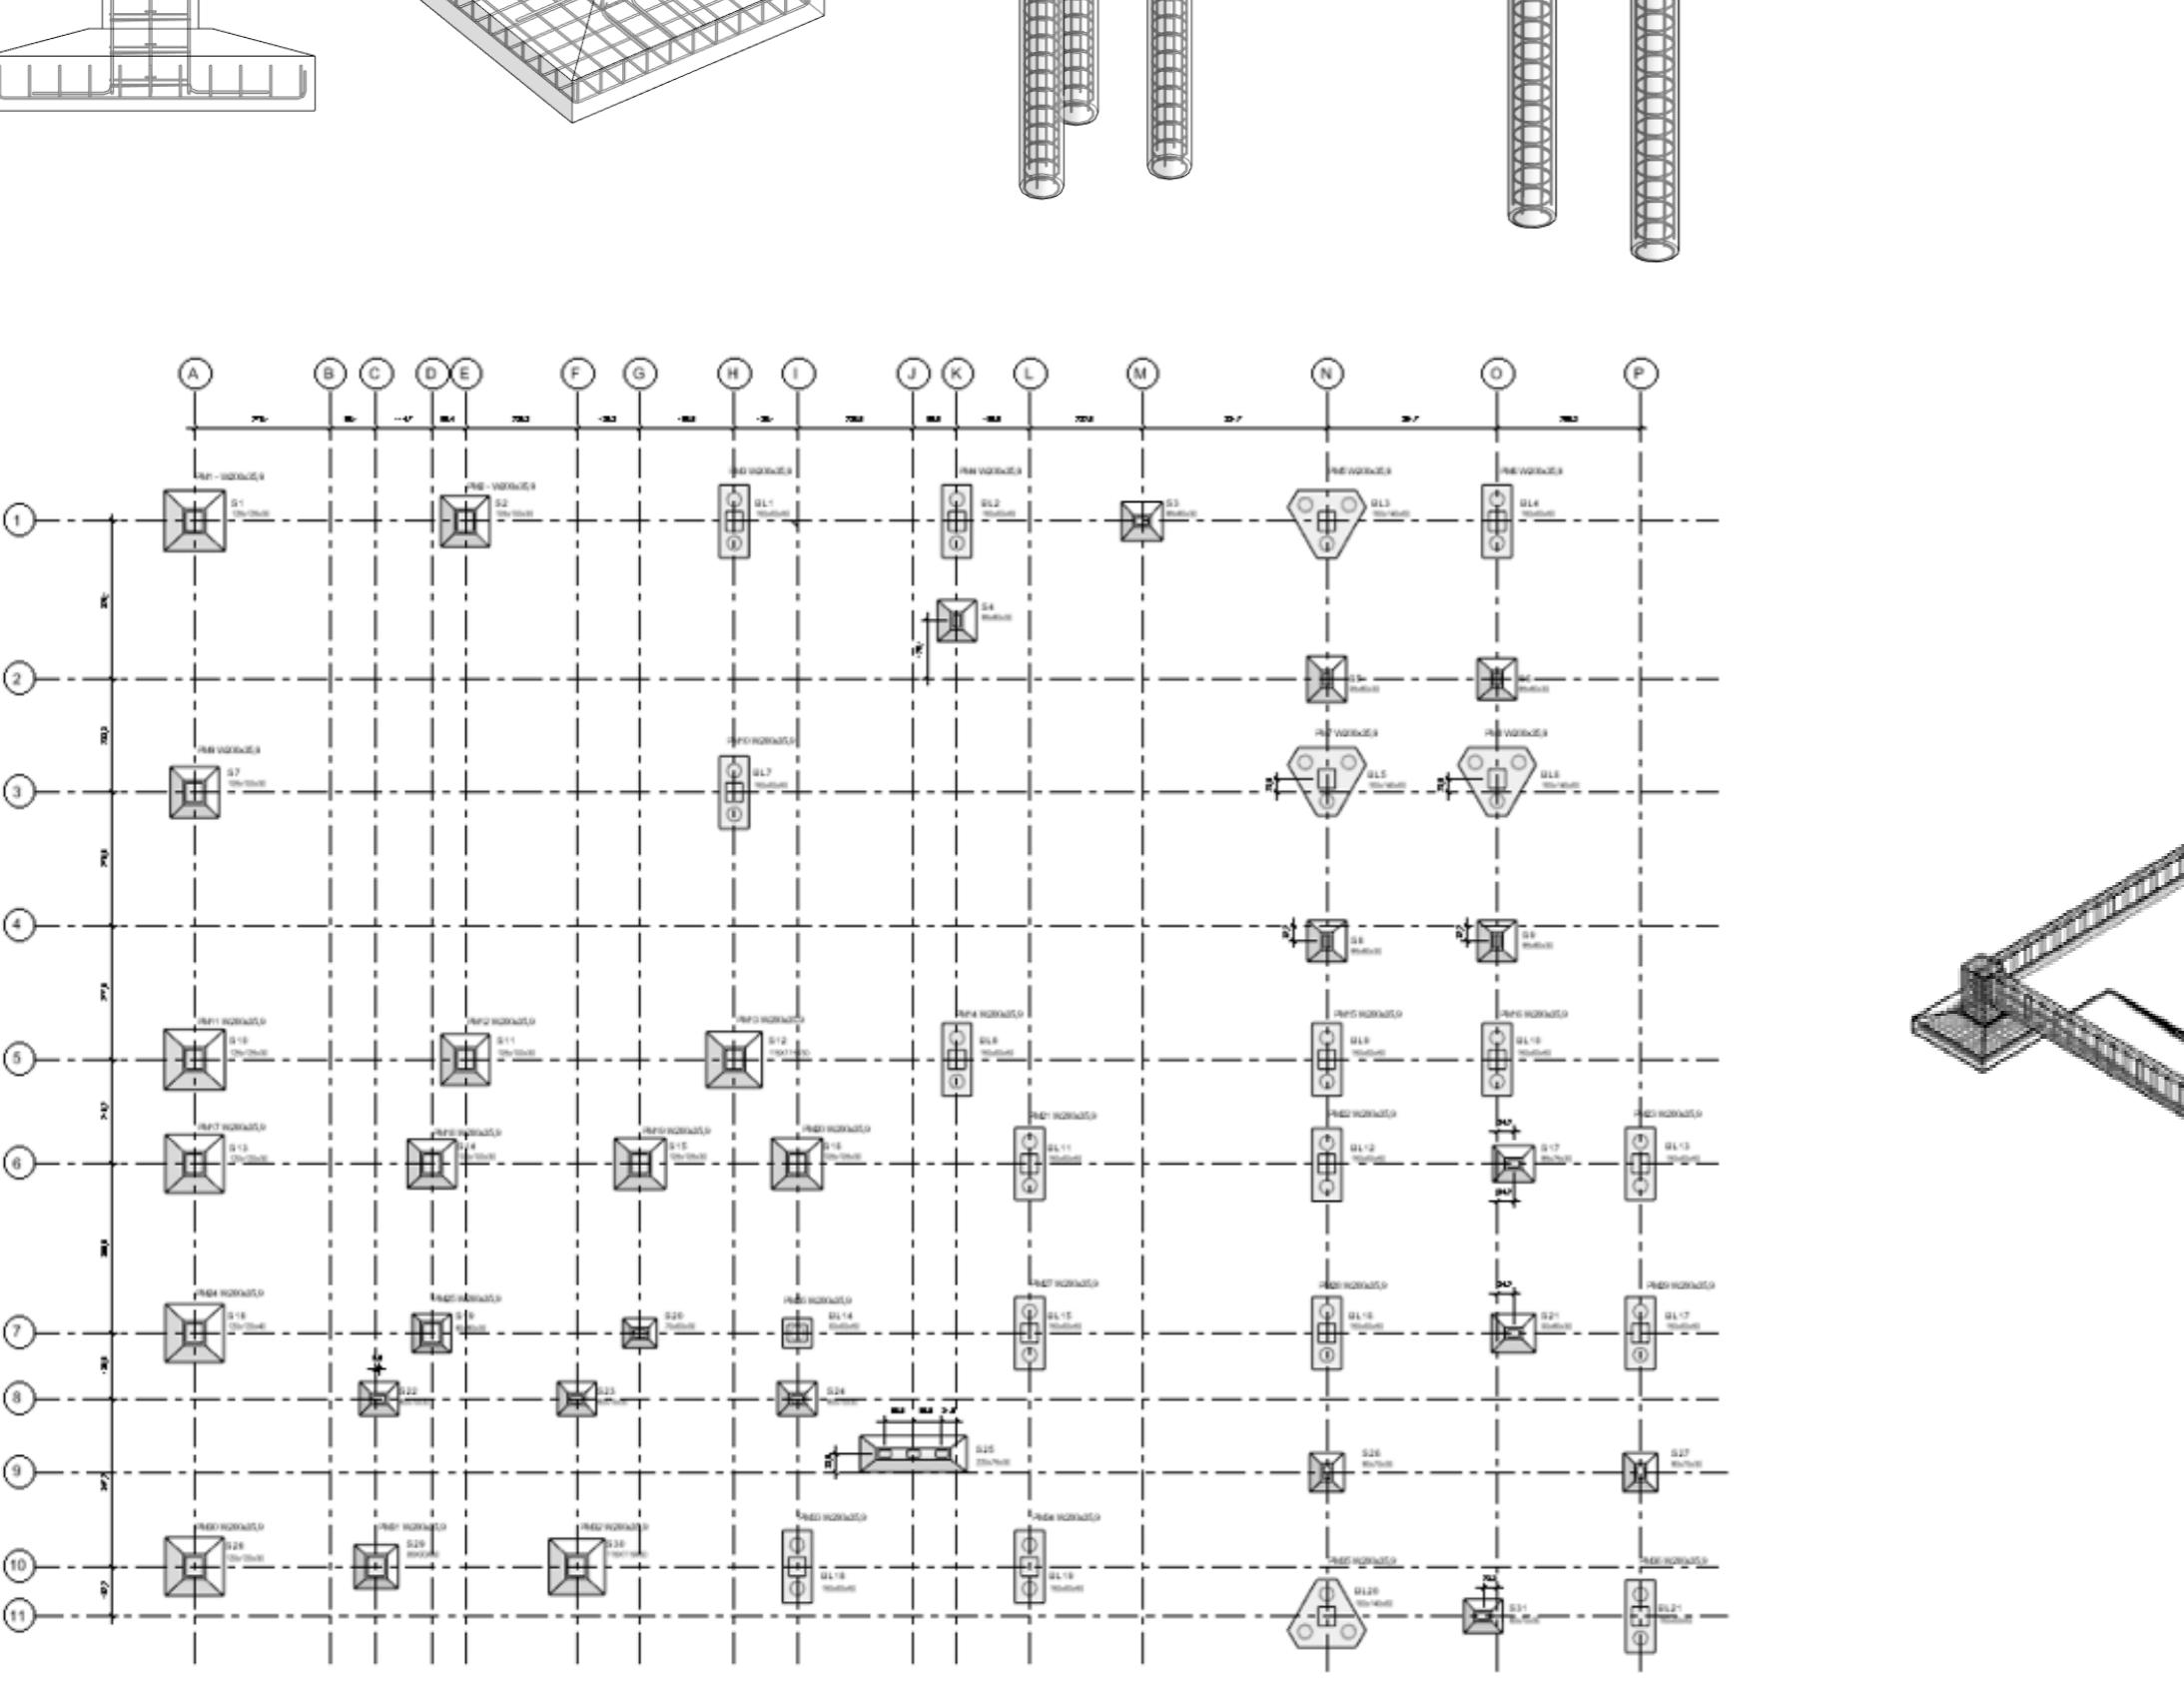

Modelagem Estrutural - Sede CREA-BA

